


AUDIO VISUAL SYSTEMS GENERAL NOTES

1. REFER TO SPECIFICATIONS FOR COMPLETE REQUIREMENTS.
2. PROVIDE CONDUIT, BOXES AND FITTINGS SHOWN ON AUDIO VISUAL SYSTEMS (AV) DRAWINGS UNDER THE WORK OF SECTION 27 05 33 COMMUNICATIONS RACEWAYS, BOXES AND FITTINGS. UNLESS OTHERWISE INDICATED, PROVIDE 1 INCH TRADE SIZE MINIMUM. PROVIDE RACEWAY SIZE AS REQUIRED FOR A MAXIMUM OF 30 PERCENT WIRE FILL.
3. PROVIDE FIRESTOPPING UNDER THE WORK OF SECTION 27 05 33.
4. LOCATIONS SHOWN ON THE ARCHITECTURAL DRAWINGS TAKE PRECEDENCE OVER LOCATIONS SHOWN ON THE COMMUNICATIONS SYSTEMS DRAWINGS.
5. DEVICE QUANTITIES SHOWN ON FLOOR PLANS AND REFLECTED CEILING PLANS TAKE PRECEDENCE OVER DEVICE QUANTITIES SHOWN ON FUNCTIONAL DIAGRAMS.
6. QUANTITIES SHOWN ON FUNCTIONAL DIAGRAMS TAKE PRECEDENCE OVER QUANTITIES SHOWN ON RACK ELEVATIONS.
7. QUANTITIES SHOWN ON DEVICE SCHEDULES TAKE PRECEDENCE OVER QUANTITIES SHOWN ON FUNCTIONAL DIAGRAMS, FLOOR PLANS AND REFLECTED CEILING PLANS.
8. LOCATIONS SHOWN ON LARGE SCALE DRAWINGS TAKE PRECEDENCE OVER LOCATIONS SHOWN ON SMALL SCALE DRAWINGS.
9. COORDINATE FINAL LOCATION OF ALL VISIBLE DEVICES WITH ARCHITECT.
10. WIRING FOR THE WORK OF AUDIO VISUAL SYSTEMS IS NOT PERMITTED TO SHARE CONDUIT, SLEEVES OR J-HOOKS WITH WIRING FOR WORK OF COMMUNICATIONS WIRES, CABLES AND RELATED. MAINTAIN AT LEAST 2 INCHES SEPARATION IF RUNNING PARALLEL. MAINTAIN AT LEAST 1 INCH OF SEPARATION VERTICALLY IF CROSSING AT RIGHT ANGLES.
11. FINAL FINISHES OF ALL VISIBLE DEVICES / SYSTEMS TO BE CONFIRMED BY ARCHITECT. FINISHES TO MATCH WALL OR CEILING ADJACENT.


ALS SCHEDULE

COMPLY WITH CBC 11B-21911B-706 ASSISTIVE-LISTENING SYSTEMS IN ASSEMBLY AREAS.		
PROVIDE COMPLETE ASSISTIVE-LISTENING SYSTEMS UNDER THE WORK OF SECTION 27 41 16.		
1A	QTY. OF PERSONAL RECEIVERS REQUIRED UNDER WORK OF SECTION 27 41 16:	
ROOM	ROOM NAME	OCCUPANTS
B1008	CLASSROOM 30 SEATS	30
B1009	CLASSROOM 30 SEATS	30
B1012	CLASSROOM 40 SEATS	40
B1013	GROUP STUDY MEDIUM (FUTURE CLASSROOM)	40
B1015	CLASSROOM 30 SEATS	30
B1016	CLASSROOM 50 SEATS	50
B1019	CLASSROOM 50 SEATS	50
B1022	CLASSROOM 50 SEATS	50
B1023	CLASSROOM 40 SEATS	40
B1026	CLASSROOM 40 SEATS	40
B10404	GROUP STUDY LARGE (FUTURE CLASSROOM)	50
1171	SMALL MEETING	19
1220	LECTURE 300	300
1220	LECTURE 150	150
1410	MEDIUM MEETING	30
1414	MEDIUM MEETING	30
1420	SOCIAL KITCHEN WORKING LOUNGE (SOUTH)	171
1455	SMALL MEETING	27
1459	MEDIUM MEETING	30
2130	SOCIAL KITCHEN WORKING LOUNGE (NORTH)	141
2133	MEDIUM MEETING	28
2161	SMALL MEETING	25
2219	SMALL MEETING	25
2350	SOCIAL KITCHEN WORKING LOUNGE (SOUTH)	143
2355	MEDIUM MEETING	32
2375	SMALL MEETING	14
2389	MEDIUM MEETING	24
2431	SMALL MEETING	15
3130	SOCIAL KITCHEN WORKING LOUNGE (NORTH)	139
3161	SMALL MEETING	26
3219	SMALL MEETING	25
3350	SOCIAL KITCHEN WORKING LOUNGE (SOUTH)	153
3355	LARGE MEETING	62
3375	SMALL MEETING	13
3389	MEDIUM MEETING	23
3431	SMALL MEETING	14
4130	SOCIAL KITCHEN WORKING LOUNGE (NORTH)	139
4161	SMALL MEETING	26
4219	SMALL MEETING	25
4350	SOCIAL KITCHEN WORKING LOUNGE (SOUTH)	178
4355	LARGE MEETING	63
4375	SMALL MEETING	14
4389	MEDIUM MEETING	23
4431	SMALL MEETING	14
5113	LARGE MEETING	40
5142	SMALL MEETING	18
5180	SOCIAL KITCHEN WORKING LOUNGE (SOUTH)	126
5310	EXTRA LARGE MEETING	64
5320	EXTRA LARGE MEETING	74
5340	EVENT SPACE	272
5360	EXTRA LARGE MEETING	46
5370	EXTRA LARGE MEETING	75
TOTAL SEATS AT ALS-REQUIRED SPACES:		3307
QUANTITY OF RECEIVERS:		69
QUANTITY OF HEARING-AID COMPATIBLE NECK LOOPS:		18
TOTAL QUANTITY OF RECEIVERS:		69
2	TYPE OF LISTENING SYSTEM: RF	
3	LOCATION: FOR USE ANYWHERE WITHIN THE ASSEMBLY AREAS.	
4	SIGNAGE: PROVIDE UNDER WORK OF SECTION 10425 SIGNS.	


LEGEND

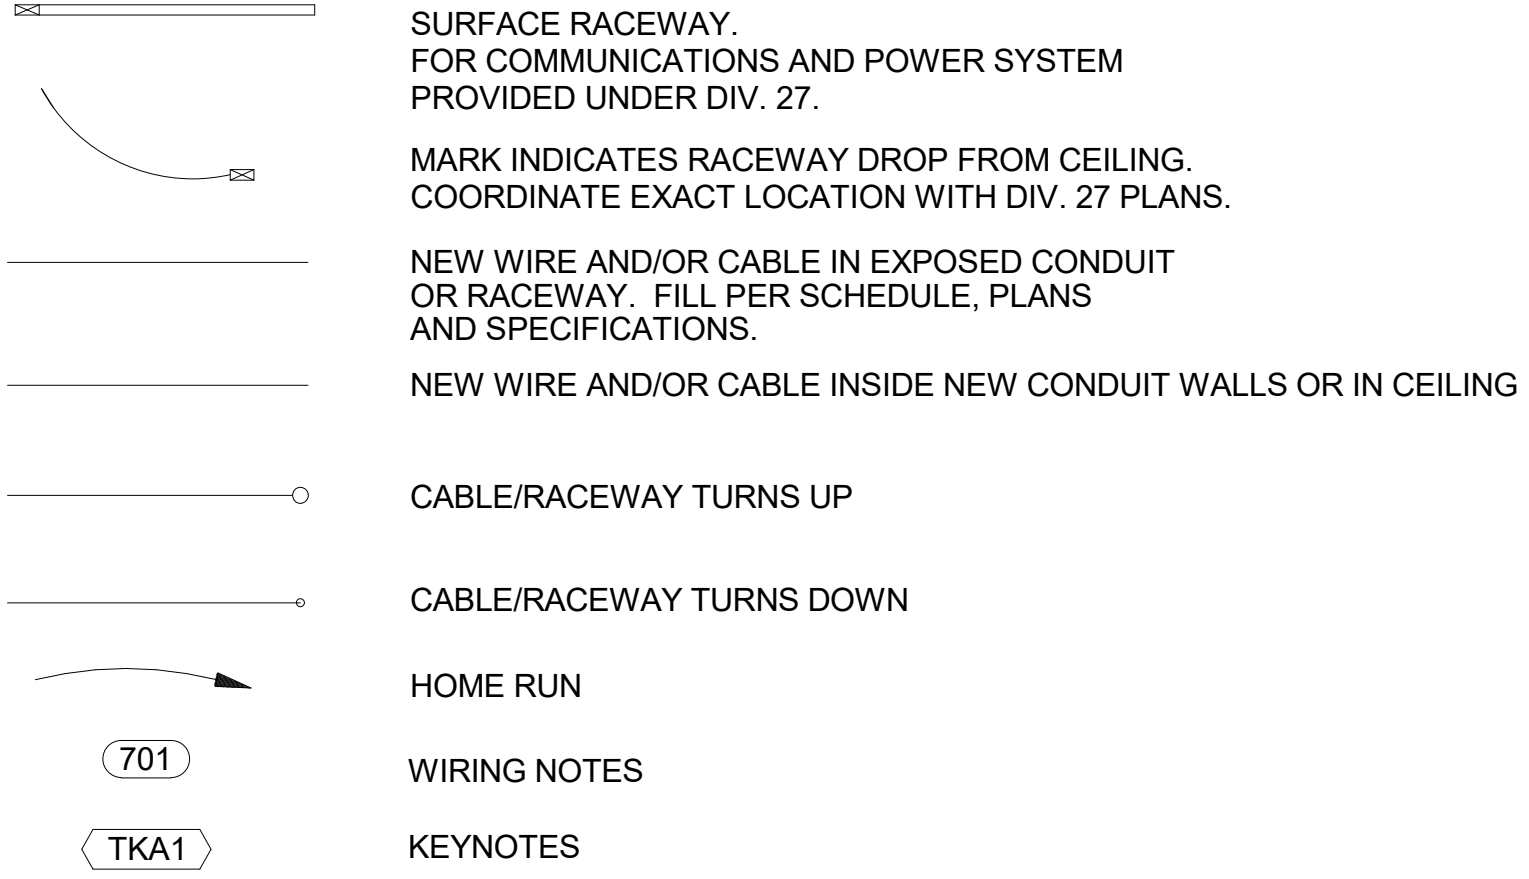

GENERAL SYMBOLS

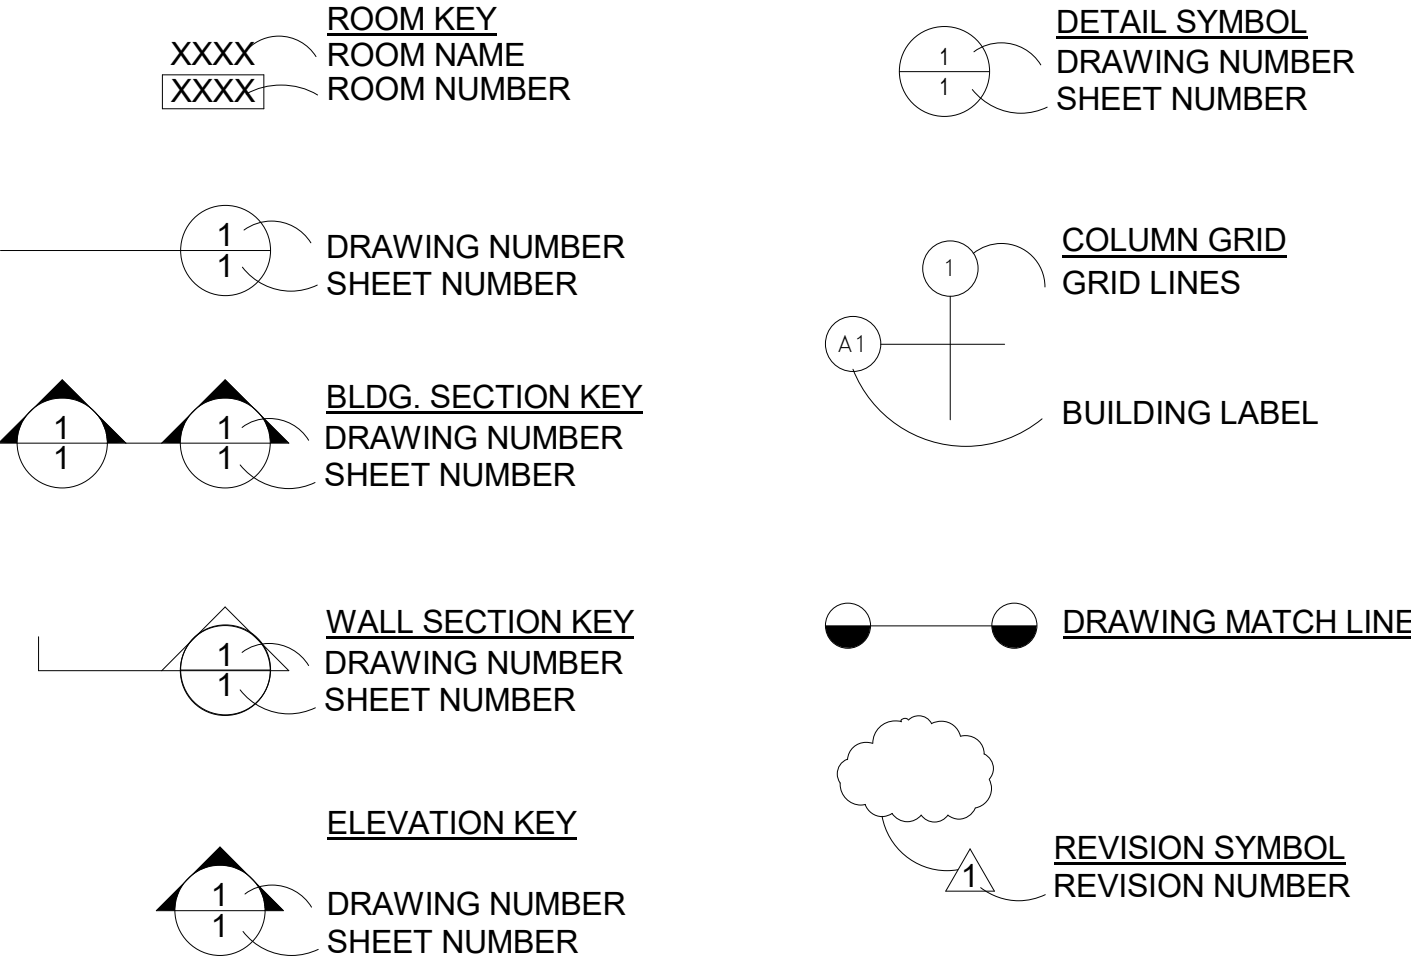

AV FUNCTIONALS LEGEND

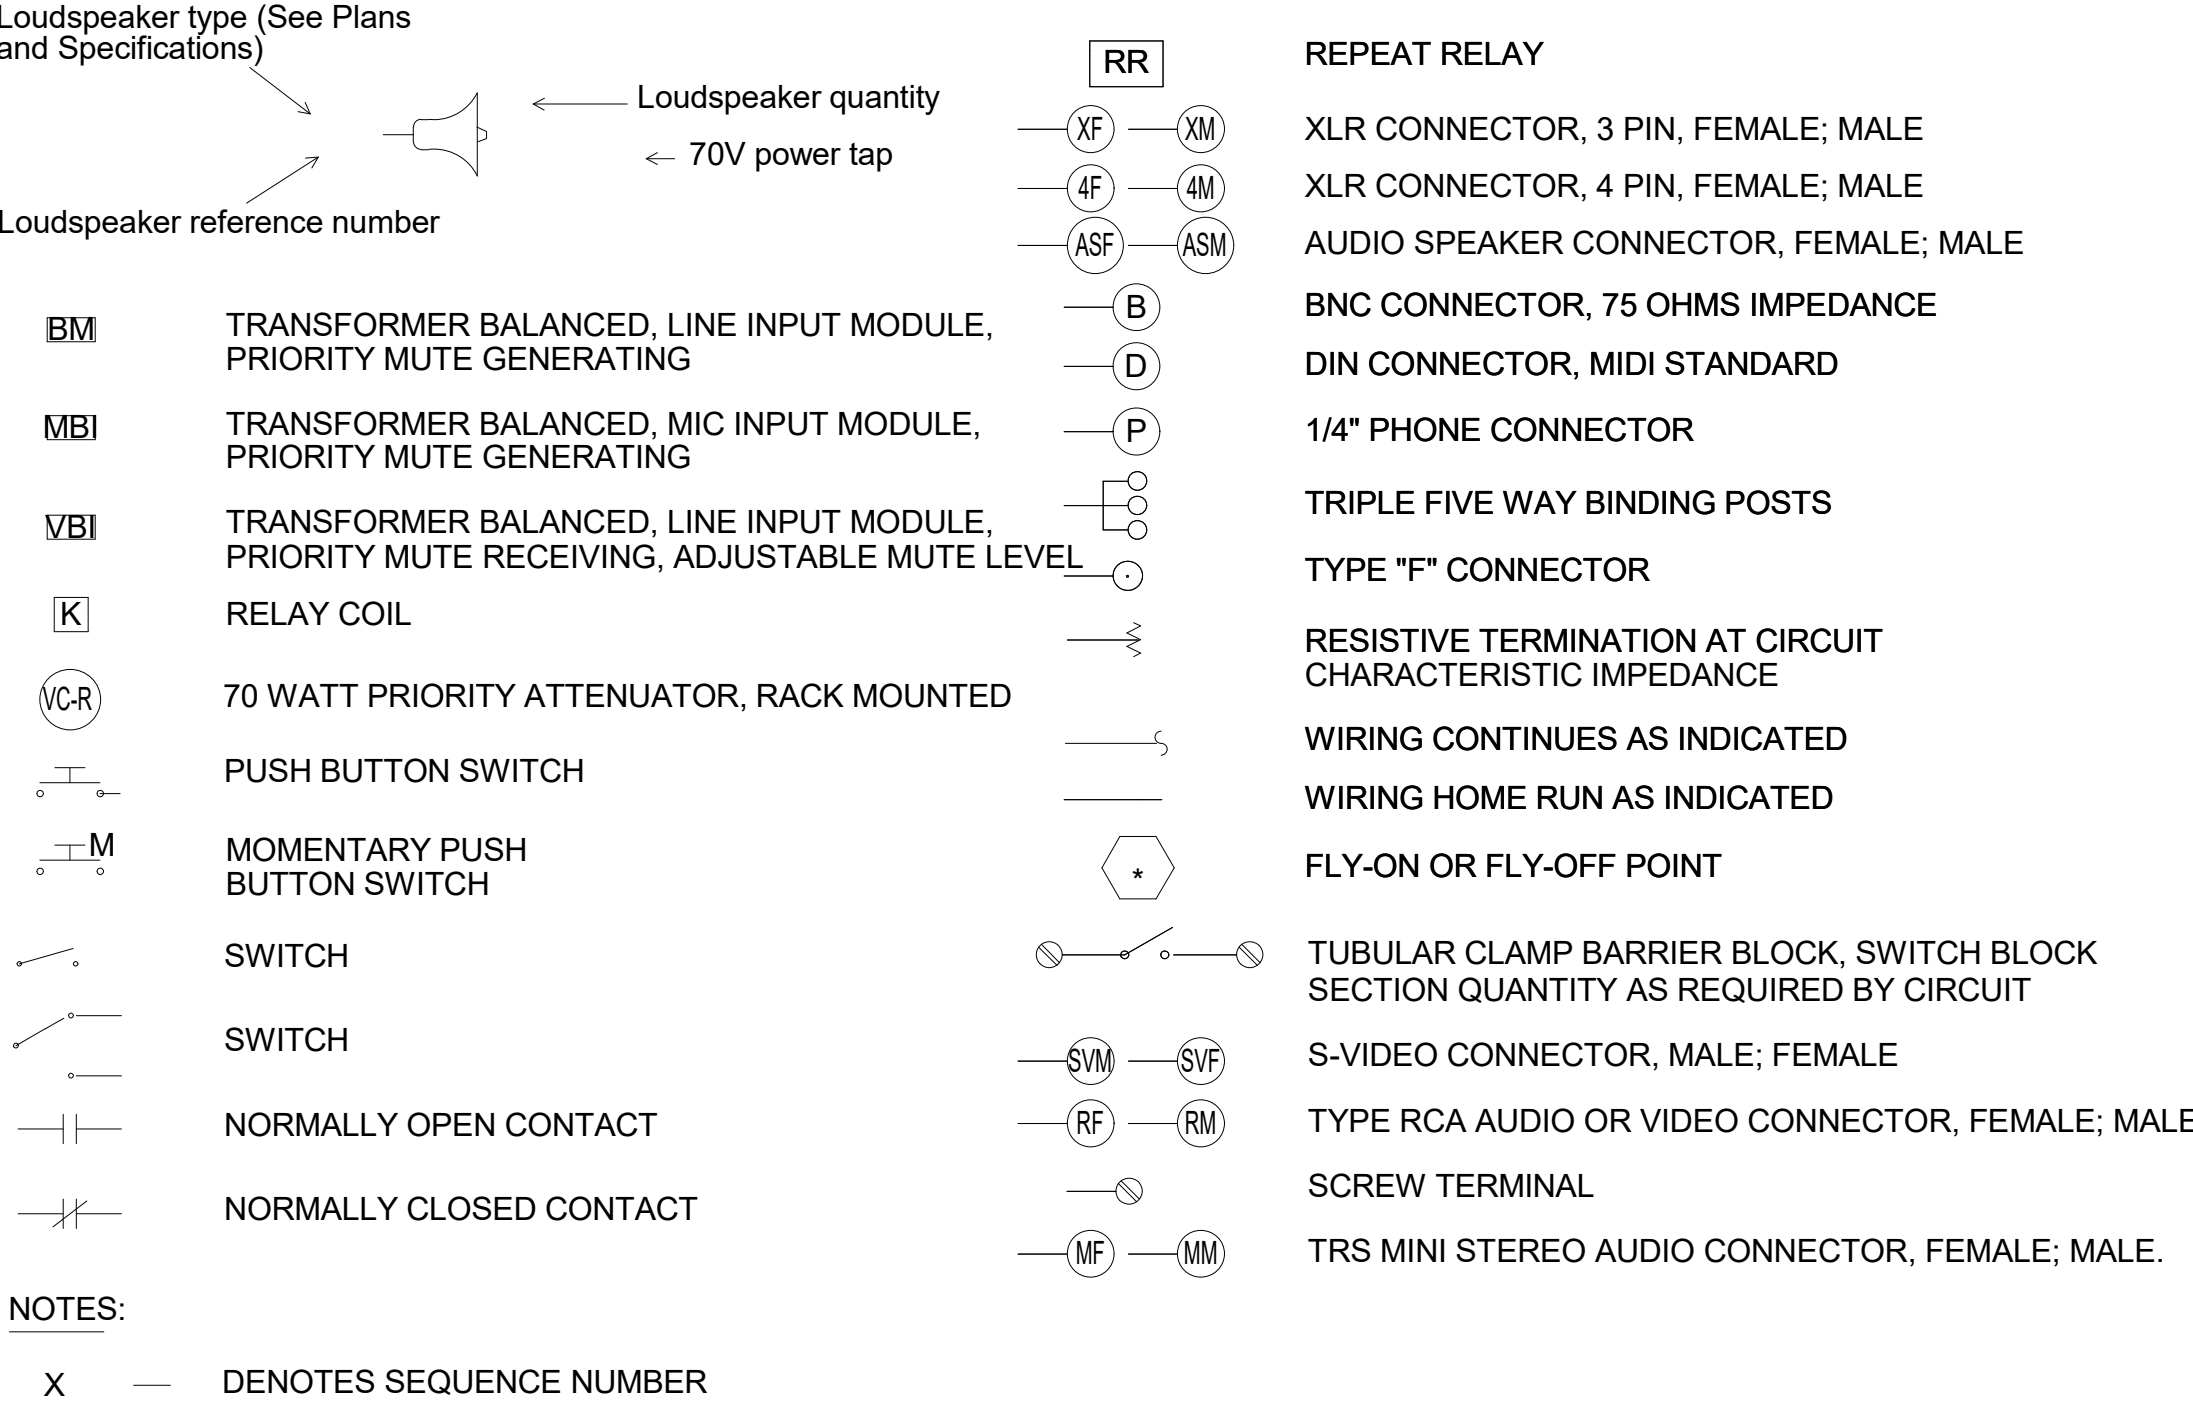

ABBREVIATIONS

A.D.A.	AMERICANS WITH DISABILITIES ACT	MMF	MULTI MODE OPTICAL FIBER
A.F.C.	ABOVE FINISHED CEILING	MOD.	MODULAR
A.F.F.	ABOVE FINISHED FLOOR	MPOE	MINIMUM POINT OF ENTRY
ALT	ALTERNATE	(N)	NEW
A.M.F.F.	ABOVE MEZZANINE FINISHED FLOOR	NEC	NATIONAL ELECTRICAL CODE
BDF	BUILDING DISTRIBUTION FACILITY	N.I.C.	NOT IN CONTRACT
B.F.C.	BELOW FINISHED CEILING	NTS	NOT TO SCALE
BLDG.	BUILDING	O.C.	ON CENTER
B.O.H.	BACK OF HOUSE	O.D.	OUTSIDE DIAMETER
C.	CONDUIT	O.F.E.	OWNER FURNISHED EQUIPMENT
CAT.	CATEGORY	OPP.	OPPOSITE
CBG	CALIFORNIA BUILDING CODE	OSP	OUTSIDE PLANT
CEC	CALIFORNIA ELECTRICAL CODE	PNL.	PANEL
COMM.	COMMUNICATIONS	PROJ.	PROJECT
C.L.	CENTERLINE	P.S.R.H.	PROJECT STANDARD RECEPTACLE HEIGHT +18" ATT. U.O.N.
C.O.	CONDUIT ONLY	P.S.S.H.	PROJECT STANDARD SWITCH HEIGHT +48" AFF TO C. U.O.N.
CONT.	CONTINUATION	RE.	REFER TO
CS	COMMUNICATIONS SYSTEM	REF.	REFERENCE
(D)	DEMOLISH EXISTING	S.A.D.	SEE ARCHITECTURAL DRAWINGS
DED	DEDUCTIVE	S.E.D.	SEE ELECTRICAL DRAWINGS
DIA.	DIAMETER	S.I.D.	SEE INTERIORS DRAWINGS
DIV	DIVISION	S.M.D.	SEE MECHANICAL DRAWINGS
(E)	EXISTING	SM.	SIMILAR
EA.	EACH	SMF	SINGLE MODE OPTICAL FIBER
EIA	ELECTRONIC INDUSTRIES ASSOCIATION	SN	SHEET NOTE
ELEV.	ELEVATION	SP	SHIELDED PAIR - SEE SPECIFICATIONS
E.O.L.	END OF LINE	SPEC	SPECIFICATION
EQPT.	EQUIPMENT	S.R.	SURFACE RACEWAY
FIN	FINISHED	STD	STANDARD
FUT	FUTURE	STP	SHIELDED TWISTED PAIR
H.R.	HOME RUN	T.C.	TELECOMMUNICATIONS CLOSET
HT.	HEIGHT	TEL	TELEPHONE
IDF	INTERMEDIATE DISTRIBUTION FACILITY	TELCOM	TELECOMMUNICATIONS
J. JBOX	JUNCTION BOX	TIA	TELECOMMUNICATIONS INDUSTRY ASSOCIATION
LAN	LOCAL AREA NETWORK	TP	TWISTED PAIR
MAX.	MAXIMUM	TYP.	TYPICAL
MDF	MAIN DISTRIBUTION FACILITY	U.O.N.	UNLESS OTHERWISE NOTED
MIN.	MINIMUM	W/	WITH
		WP	WEATHERPROOF

JUNCTION BOX SCHEDULE

SYMBOL	H (INCHES)	W (INCHES)	D (INCHES)
J1	6	6	4
J2	8	8	4
J3	12	12	4
J4	12	12	6
J5	12	12	8
J6	16	12	8
J7	18	18	6
J8	20	16	6
J9	20	16	8
J10	20	20	6
J11	20	20	8
J12	24	20	6
J13	24	20	8
J14	24	24	8
J15	30	24	8
J16	30	30	8
J17	36	30	8
J18	36	36	8

SUFFIX:
NONE - NEMA 1
A - NEMA 12
B - NEMA 3R
C - NEMA 4
D - NEMA 4X

NOTE:
ALL JUNCTION BOXES TO BE HINGED TYPE, PROVIDED WITHOUT PRE-PUNCHED KNOCKOUTS, PENETRATIONS IN JUNCTION BOXES SHALL BE CUT OR PUNCHED AS REQUIRED FOR INSTALLATION. PAINT ALL INTERIOR BOXES TO MATCH WALL FINISH. COORDINATE FINISH WITH ARCH. PLANS.

AUDIOVISUAL DRAWING LIST	
SHEET NO.	SHEET NAME
TA0.001	GENERAL NOTES, LEGEND, SYMBOLS, ABBREVIATIONS AND JBOX SCHEDULE
TA0.002	SYMBOL SCHEDULE
TA1.100A	AUDIOVISUAL PLAN LOWER LEVEL - SECTOR WEST
TA1.101A	AUDIOVISUAL PLAN LEVEL 1 - SECTOR WEST
TA1.101C	AUDIOVISUAL PLAN LEVEL 1 - SECTOR EAST
TA1.102A	AUDIOVISUAL PLAN LEVEL 2 - SECTOR WEST
TA1.102C	AUDIOVISUAL PLAN LEVEL 2 - SECTOR EAST
TA1.103A	AUDIOVISUAL PLAN LEVEL 3 - SECTOR WEST
TA1.103C	AUDIOVISUAL PLAN LEVEL 3 - SECTOR EAST
TA1.104A	AUDIOVISUAL PLAN LEVEL 4 - SECTOR WEST
TA1.104C	AUDIOVISUAL PLAN LEVEL 4 - SECTOR EAST
TA1.105A	AUDIOVISUAL PLAN LEVEL 5 - SECTOR WEST
TA1.105C2	AUDIOVISUAL PLAN LEVEL 5 - SECTOR EAST - ALTERNATE
TA1.400A	AUDIOVISUAL RCP LOWER LEVEL - SECTOR WEST
TA1.401A	AUDIOVISUAL RCP LEVEL 1 - SECTOR WEST
TA1.401C	AUDIOVISUAL RCP LEVEL 1 - SECTOR EAST
TA1.402A	AUDIOVISUAL RCP LEVEL 2 - SECTOR WEST
TA1.402C	AUDIOVISUAL RCP LEVEL 2 - SECTOR EAST
TA1.403A	AUDIOVISUAL RCP LEVEL 3 - SECTOR WEST
TA1.403C	AUDIOVISUAL RCP LEVEL 3 - SECTOR EAST
TA1.404A	AUDIOVISUAL RCP LEVEL 4 - SECTOR WEST
TA1.404C	AUDIOVISUAL RCP LEVEL 4 - SECTOR EAST
TA1.405A	AUDIOVISUAL RCP LEVEL 5 - SECTOR WEST
TA1.405C2	AUDIOVISUAL RCP LEVEL 5 - SECTOR EAST - ALTERNATE
TAS.000	AUDIOVISUAL ENLARGED PLANS, RCP & ELEVATIONS
TAS.001	AUDIOVISUAL ENLARGED PLANS, RCP & ELEVATIONS
TAS.002	AUDIOVISUAL ENLARGED PLANS, RCP & ELEVATIONS
TAS.003	AUDIOVISUAL ENLARGED PLANS, RCP & ELEVATIONS
TAS.004	AUDIOVISUAL ENLARGED PLANS, RCP & ELEVATIONS
TAS.005	AUDIOVISUAL ENLARGED PLANS, RCP & ELEVATIONS
TAS.006	AUDIOVISUAL ENLARGED PLANS, RCP & ELEVATIONS
TAS.100	AUDIOVISUAL ENLARGED PLANS, RCP & ELEVATIONS
TAS.101	AUDIOVISUAL ENLARGED PLANS, RCP & ELEVATIONS
TAS.102	AUDIOVISUAL ENLARGED PLANS, RCP & ELEVATIONS
TAS.103	AUDIOVISUAL ENLARGED PLAN, RCP & ELEVATION
TAS.104	AUDIOVISUAL ENLARGED PLAN, RCP & ELEVATION
TAS.105	AUDIOVISUAL ENLARGED PLAN, RCP & ELEVATION
TAS.106	AUDIOVISUAL ENLARGED PLAN, RCP & ELEVATION
TAS.200	AUDIOVISUAL ENLARGED PLANS, RCP & ELEVATIONS
TAS.201	AUDIOVISUAL ENLARGED PLANS, RCP & ELEVATIONS
TAS.202	AUDIOVISUAL ENLARGED PLANS, RCP & ELEVATIONS
TAS.203	AUDIOVISUAL ENLARGED PLANS, RCP & ELEVATIONS
TAS.204	AUDIOVISUAL ENLARGED PLANS, RCP & ELEVATIONS
TAS.205	AUDIOVISUAL ENLARGED PLAN, RCP & ELEVATION
TAS.206	AUDIOVISUAL ENLARGED PLAN, RCP & ELEVATION
TAS.207	AUDIOVISUAL ENLARGED PLANS, RCP & ELEVATIONS
TAS.300	AUDIOVISUAL ENLARGED PLANS, RCP & ELEVATIONS
TAS.301	AUDIOVISUAL ENLARGED PLANS, RCP & ELEVATIONS
TAS.302	AUDIOVISUAL ENLARGED PLANS, RCP & ELEVATIONS
TAS.303	AUDIOVISUAL ENLARGED PLANS, RCP & ELEVATIONS
TAS.304	AUDIOVISUAL ENLARGED PLANS, RCP & ELEVATIONS
TAS.305	AUDIOVISUAL ENLARGED PLAN, RCP & ELEVATION
TAS.306	AUDIOVISUAL ENLARGED PLAN, RCP & ELEVATION
TAS.307	AUDIOVISUAL ENLARGED PLANS, RCP & ELEVATIONS
TAS.400	AUDIOVISUAL ENLARGED PLANS, RCP & ELEVATIONS
TAS.401	AUDIOVISUAL ENLARGED PLANS, RCP & ELEVATIONS
TAS.402	AUDIOVISUAL ENLARGED PLANS, RCP & ELEVATIONS
TAS.403	AUDIOVISUAL ENLARGED PLANS, RCP & ELEVATIONS
TAS.404	AUDIOVISUAL ENLARGED PLANS, RCP & ELEVATIONS
TAS.405	AUDIOVISUAL ENLARGED PLAN, RCP & ELEVATION
TAS.406	AUDIOVISUAL ENLARGED PLAN, RCP & ELEVATION
TAS.407	AUDIOVISUAL ENLARGED PLANS, RCP & ELEVATIONS
TAS.500	AUDIOVISUAL ENLARGED PLANS, RCP & ELEVATIONS
TAS.501	AUDIOVISUAL ENLARGED PLANS, RCP & ELEVATIONS
TAS.502	AUDIOVISUAL ENLARGED PLANS, RCP & ELEVATIONS
TAS.503	AUDIOVISUAL ENLARGED PLAN, RCP & ELEVATION
TAS.504	AUDIOVISUAL ENLARGED PLAN & ELEVATION
TAS.505	AUDIOVISUAL ENLARGED RCP & ELEVATION
TAS.601	AUDIOVISUAL PLAN & RCP - LOWER LEVEL - ADDITIVE BID ALTERNATE (RECORDING STUDIO)
TA7.000	AUDIOVISUAL ROOM SCHEDULE
TA7.001	AUDIOVISUAL RISER SINGLE LINE DIAGRAM
TA7.002	AUDIOVISUAL FUNCTIONAL DIAGRAMS
TA7.003	SMALL MEETING ROOM AUDIOVISUAL FUNCTIONAL DIAGRAM
TA7.004	MEDIUM MEETING ROOM AUDIOVISUAL FUNCTIONAL DIAGRAM
TA7.005	RECORDING SUITE AV BACKBONE
TA7.006	RECORDING STUDIO & PRODUCTION FUNCTIONAL DIAGRAMS
TA7.007	GROUP STUDY LARGE B10404 AUDIOVISUAL FUNCTIONAL DIAGRAMS
TA7.008	GROUP STUDY MEDIUM B1015 AUDIOVISUAL FUNCTIONAL DIAGRAMS
TA7.100	TYPICAL CLASSROOM AUDIOVISUAL FUNCTIONAL DIAGRAM
TA7.101	TYPICAL CLASSROOM AUDIOVISUAL FUNCTIONAL DIAGRAM LLT SOUTH
TA7.102	SOCIAL KITCHEN WORKING LOUNGE 1420 AUDIOVISUAL FUNCTIONAL DIAGRAM
TA7.103	LECTURE HALL 300 1210 AUDIOVISUAL FUNCTIONAL DIAGRAM
TA7.104	LECTURE HALL 150 1220 AUDIOVISUAL FUNCTIONAL DIAGRAM
TA7.105	CAPL 1310 AUDIOVISUAL FUNCTIONAL DIAGRAM
TA7.106	SOUTH VITRENE VIDEO WALL AUDIOVISUAL FUNCTIONAL DIAGRAM
TA7.107	NORTH VITRENE VIDEO WALL AUDIOVISUAL FUNCTIONAL DIAGRAM
TA7.201	SOCIAL KITCHEN WORKING LOUNGE 2130 AUDIOVISUAL FUNCTIONAL DIAGRAM
TA7.202	SOCIAL KITCHEN WORKING LOUNGE 2350 MEDIUM MEETING 2355 AUDIOVISUAL FUNCTIONAL DIAGRAM
TA7.301	SOCIAL KITCHEN WORKING LOUNGE 3130 AUDIOVISUAL FUNCTIONAL DIAGRAM
TA7.302	SOCIAL KITCHEN WORKING LOUNGE 3350 LARGE MEETING 3391 AUDIOVISUAL FUNCTIONAL DIAGRAM
TA7.401	SOCIAL KITCHEN WORKING LOUNGE 4130 AUDIOVISUAL FUNCTIONAL DIAGRAM
TA7.402	SOCIAL KITCHEN WORKING LOUNGE 4350 LARGE MEETING 4391 AUDIOVISUAL FUNCTIONAL DIAGRAM
TA7.501	LARGE/EXTRA-LARGE MEETING
TA7.502	LARGE MEETING 5100-5110-5440 AUDIOVISUAL FUNCTIONAL DIAGRAM
TA7.503	SOCIAL KITCHEN WORKING LOUNGE 5220 AUDIOVISUAL FUNCTIONAL DIAGRAM
TA7.504	GREEN ROOM 5327 & EVENT SPACE 5440 AUDIOVISUAL FUNCTIONAL DIAGRAM
TA7.505	LARGE MEETING 5310 & 5320 AUDIOVISUAL FUNCTIONAL DIAGRAM
TA0.001	DETAILS - FLOOR BOX
TA0.002	DETAILS - FLAT PANEL WALL BOX AND FLAT PANEL MOUNT
TA0.003	DETAILS - RACK R18
TA0.004	DETAILS - RACK R33
TA0.005	DETAILS - RACK R35
TA0.006	DETAILS - INTERIOR FASTENING



UCB Gateway Building
Berkeley CA 94720

WEISS / MANFREDI + GENSLER

DESIGN ARCHITECT
Weiss Manfredi
220 Hudson St. 10th Floor
NY, NY 10013
United States
Tel 212.760.9002
Fax 212.760.9003

STRUCTURAL ENGINEER
MKA
1301 Fifth Avenue Suite 3200
Seattle, WA 98101
United States
Tel 206.292.1200
Fax xxx.xxx.xxx

CIVIL ENGINEER
Shenwood Engineers
2548 Mission St.
San Francisco, CA 94110
United States
Tel 415.677.2300
Fax xxx.xxx.xxx

LIGHTING
Auerbach Giesow
1045 Sansome St., Suite 300
Seattle, WA 98101
United States
Tel 415.392.3238
Fax 415.392.7530

AVIT
SFM
351 Br. St.
San Francisco, CA 94103
United States
Tel 415.255.9140
Fax 415.255.9180

ELEVATOR
Syska Hennessy
425 California St., Suite 400
San Francisco, CA 94104
United States
Tel 415.288.5061
Fax xxx.xxx.xxx

LANDSCAPE
PGA Design
444 17th Street
Oakland, CA 94612
United States
Tel 510.465.1284
Fax 510.465.1286

BUILDING MAINTENANCE
STICO
183A Beacon St.
South San Francisco, CA 94080
United States
Tel 650.588.4626

WIND ENGINEERING
RWI
203-1480 Blvd de l'Innovation
Bromont, Quebec J2L 0J8
Canada
Tel 450.534.1007
Fax 519.623.1316

HARDWARE
DCT
14872 San Juan Ave. Ste 212
Dana Point, CA 92629
United States
Tel 949.368.6571

MECHANICAL (TRADE)
ACCDES
1133 Aladdin Ave
San Leandro, CA 94577
United States
Tel 510.346.4300

FIRE PROTECTION (TRADE)
Pribus
523 Mayfair Ave
South SF CA 94080
United States
Tel 650.588.2968

Date	Description
2022/05/18	UCB GATEWAY DESIGN DEVELOPMENT 100%
2022/08/10	UCB GATEWAY CONSTRUCTION DOCS 95%
2022/10/12	UCB GATEWAY CONSTRUCTION DOCS 95%
2022/12/02	UCB GATEWAY CONSTRUCTION DOCS 100%
2023/03/29	PERMIT PLAN CHECK #3

Seal / Signature

DATE 03/24/23
RAY ENWORTH
REG. NO. 10611
EXPIRES 12/31/2025

Project Name
UCB Gateway


Project Number
01.4968.000

Description
GENERAL NOTES, LEGEND, SYMBOLS, ABBREVIATIONS AND JBOX SCHEDULE


Scale

TA0.001

3/27/2023 9:35:43 AM BM\351\0714988.00 - UCS Gateway Technology - 01.4968.00 - UCS Gateway.rvt

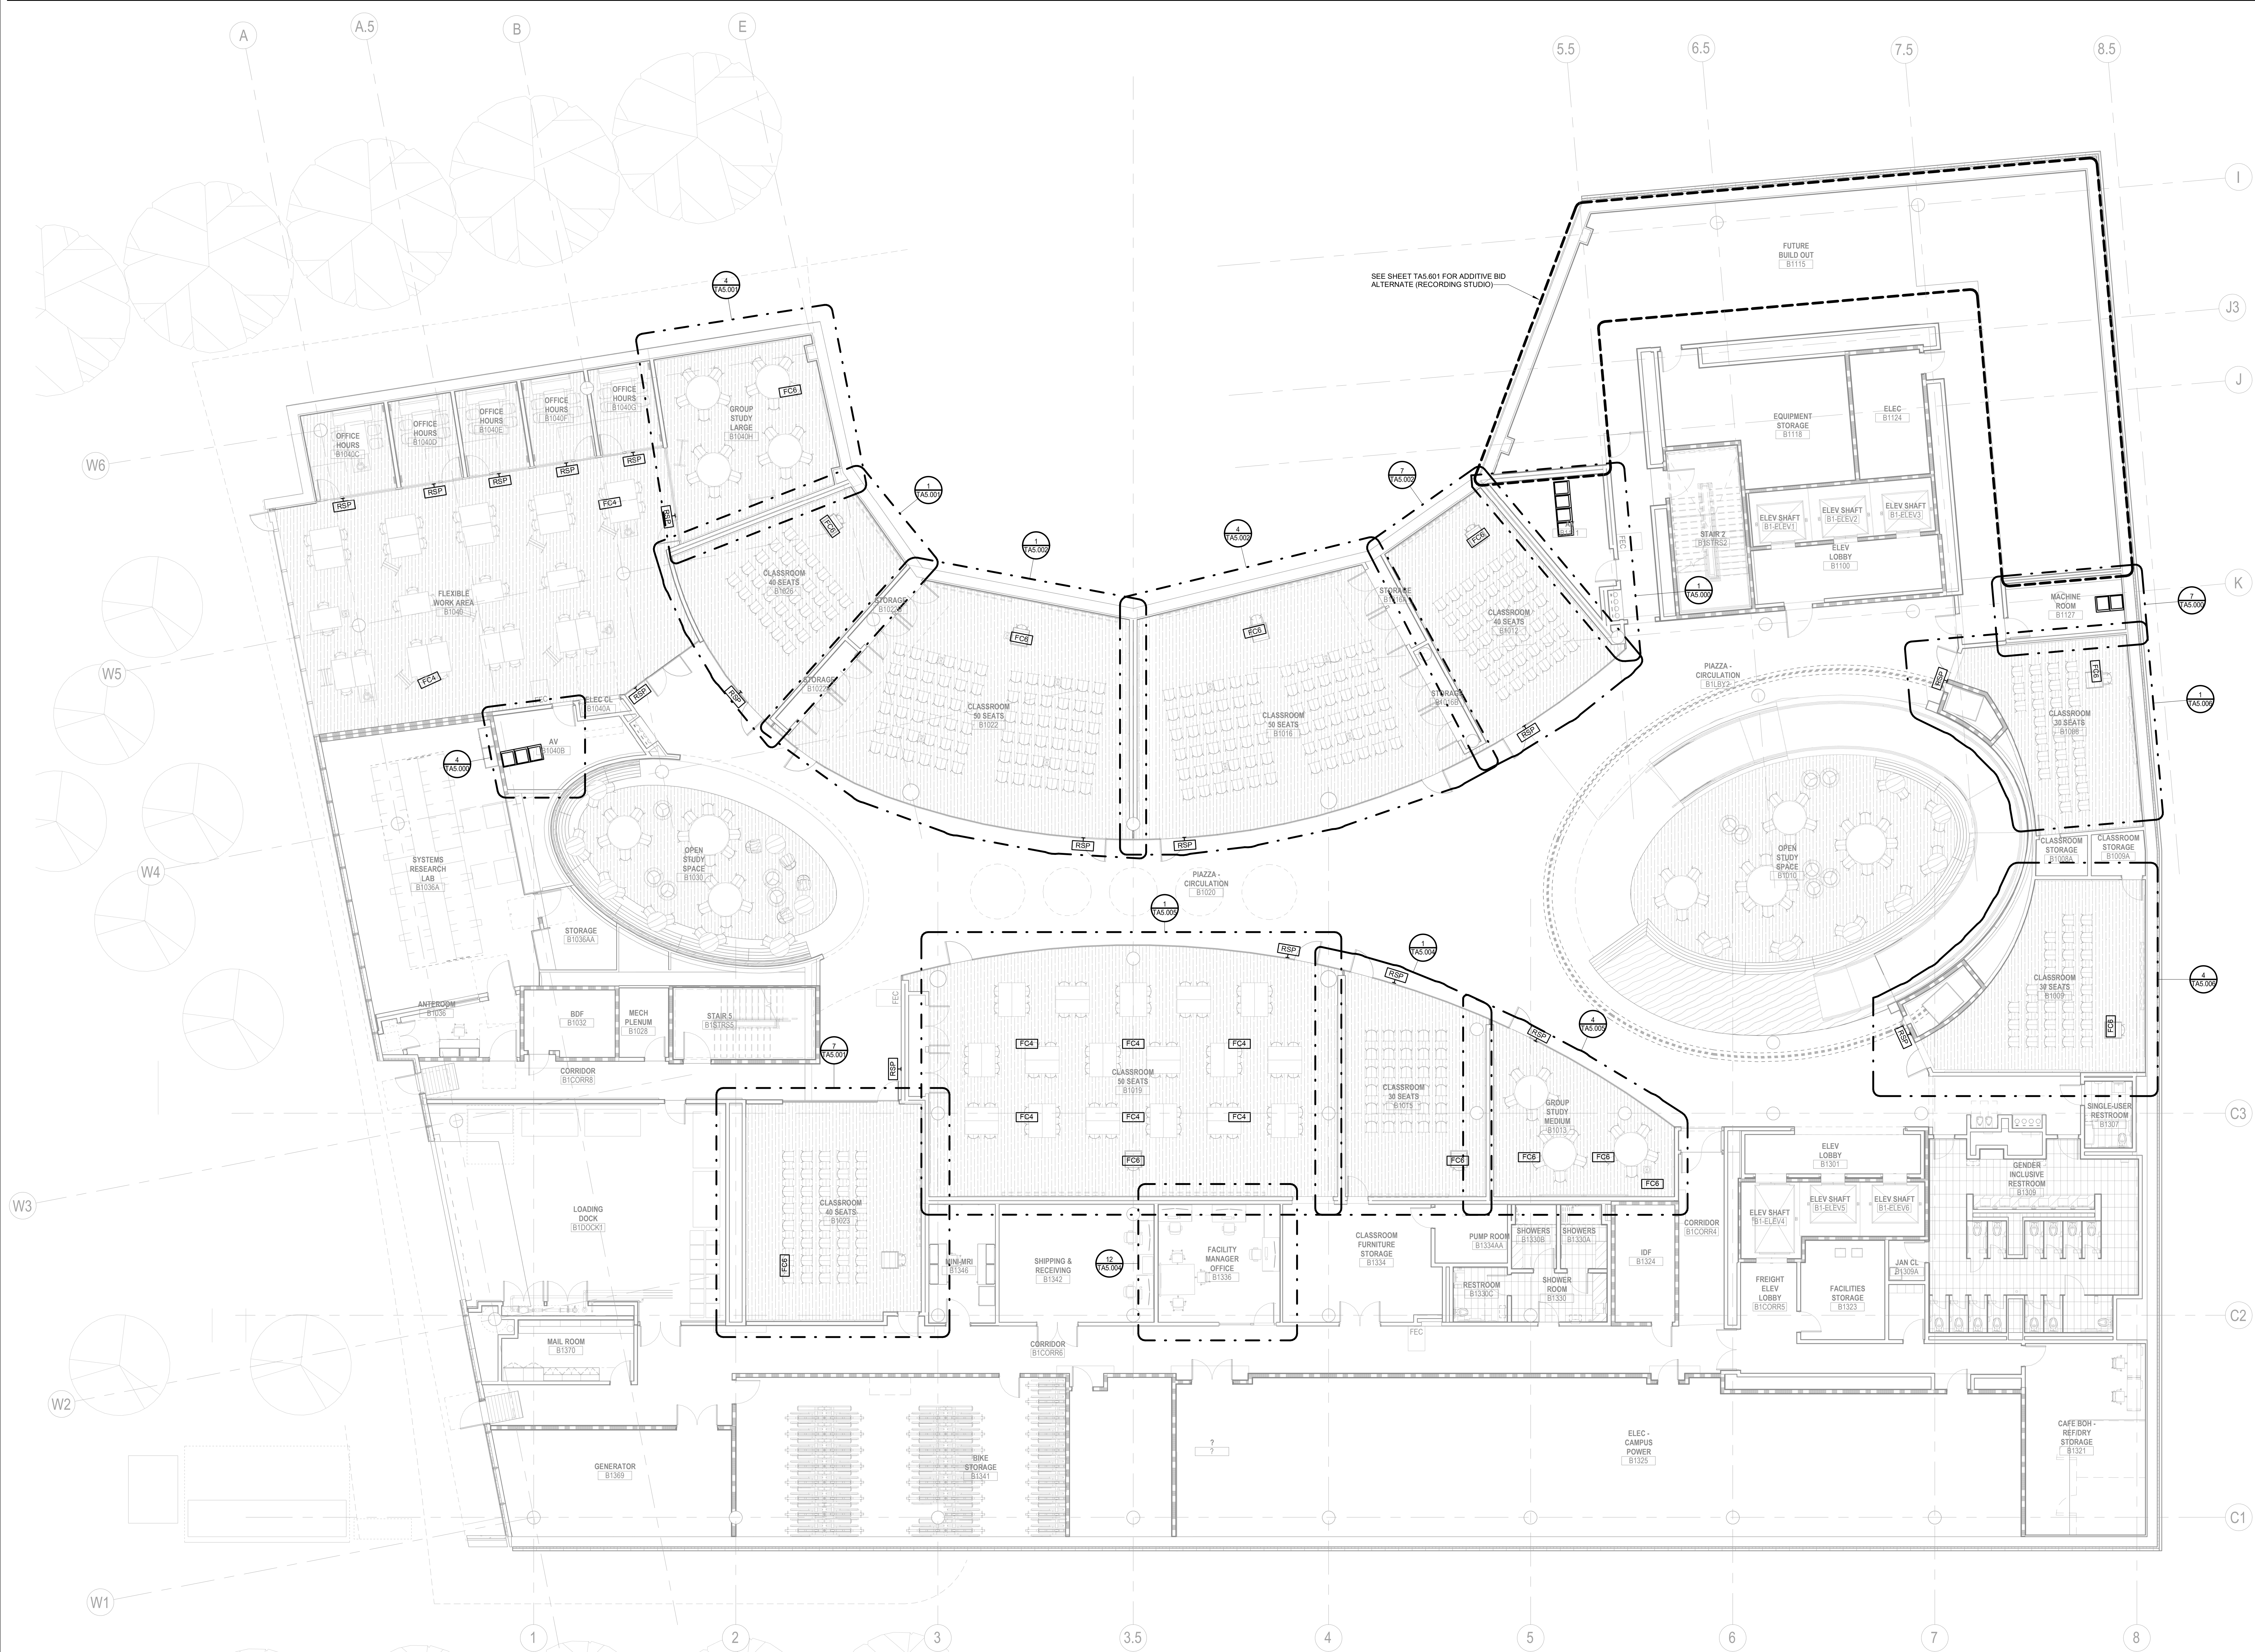

KEYNOTES

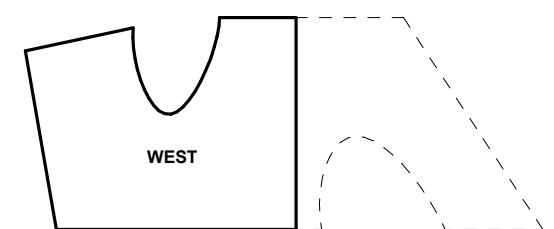

UCB Gateway Building
Berkeley CA 94720

WEISS / MANFREDI + GENSLER

DESIGN ARCHITECT
Weiss Manfredi
220 Hudson St. 10th Floor
NY, NY 10013
United States
Tel 212.760.9002
Fax 212.760.9003

EXECUTIVE ARCHITECT
Gensler
45 Fremont St. Suite 1500
San Francisco, CA 94105
United States
Tel 415.433.3700
Fax 415.636.4599

STRUCTURAL ENGINEER
AKA
1301 Fifth Avenue Suite 3200
Seattle, WA 98101
United States
Tel 206.292.1200
Fax xxx.xxx.xxxx

CIVIL ENGINEER
Shenwood Engineers
2548 Mission St.
San Francisco, CA 94110
United States
Tel 415.677.7200
Fax xxx.xxx.xxxx

COST ESTIMATING
TBD Consultants
111 Pine St. Suite 1315
San Francisco, CA 94111
United States
Tel 415.391.7610
Fax 415.981.9434

ACUSTIC, SECURITY
Shen, Misson, Wilke
351 California St. Suite 810
San Francisco, CA 94104
United States
Tel 415.392.7328
Fax 415.392.7330

AVIT
SFM
351 Br. St.
San Francisco, CA 94103
United States
Tel 415.392.9140
Fax xxx.xxx.xxxx

ELEVATOR
Syka Hennessey
425 California St. Suite 400
San Francisco, CA 94104
United States
Tel 415.288.9061
Fax xxx.xxx.xxxx

LANDSCAPE
PGA Design
444 17th Street
Oakland, CA 94612
United States
Tel 510.465.1284
Fax 510.465.1286

BUILDING MAINTENANCE
STICO
183A Beacon St
South San Francisco, CA
94080
United States
Tel 650.586.4626

WIND ENGINEERING
RWI
203-1460 Blvd de l'Innovation
Bromont, Quebec J2L 0J8
Canada
Tel 450.534.1007
Fax 519.623.1316

HARDWARE
DCI
24072 San Juan Ave. Ste 212
Dana Point, CA, 92629
United States
Tel 949.368.6571

MECHANICAL (TRADE)
ACCDES
1133 Alameda Ave
San Leandro, CA, 94577
United States
Tel 510.345.4300

FIRE PROTECTION (TRADE)
Pribuss
523 Mayfair Ave
South SF CA, 94080
United States
Tel 650.586.2968

WATERPROOFING
WUE
2000 Powell Street
Suite 1650
Emeryville, CA 94608
Tel 510.428-2907

ELECTRICAL (TRADE)
CEI
1132 N 7th St
San Jose, CA, 95112
United States
Tel 408.388.8000

PLUMBING (TRADE)
Frank M Booth
251 Michelle Ct
South SF, CA 94080
United States
Tel 650.359.1844

DATE 03/24/23
DATE 03/24/23
DATE 03/24/23

Project Name
UCB Gateway


Project Number
01.4968.000

Description
AUDIOVISUAL PLAN LOWER LEVEL -
SECTOR WEST


Scale
1/8" = 1'-0"

TA1.100A


© 2022 Gensler

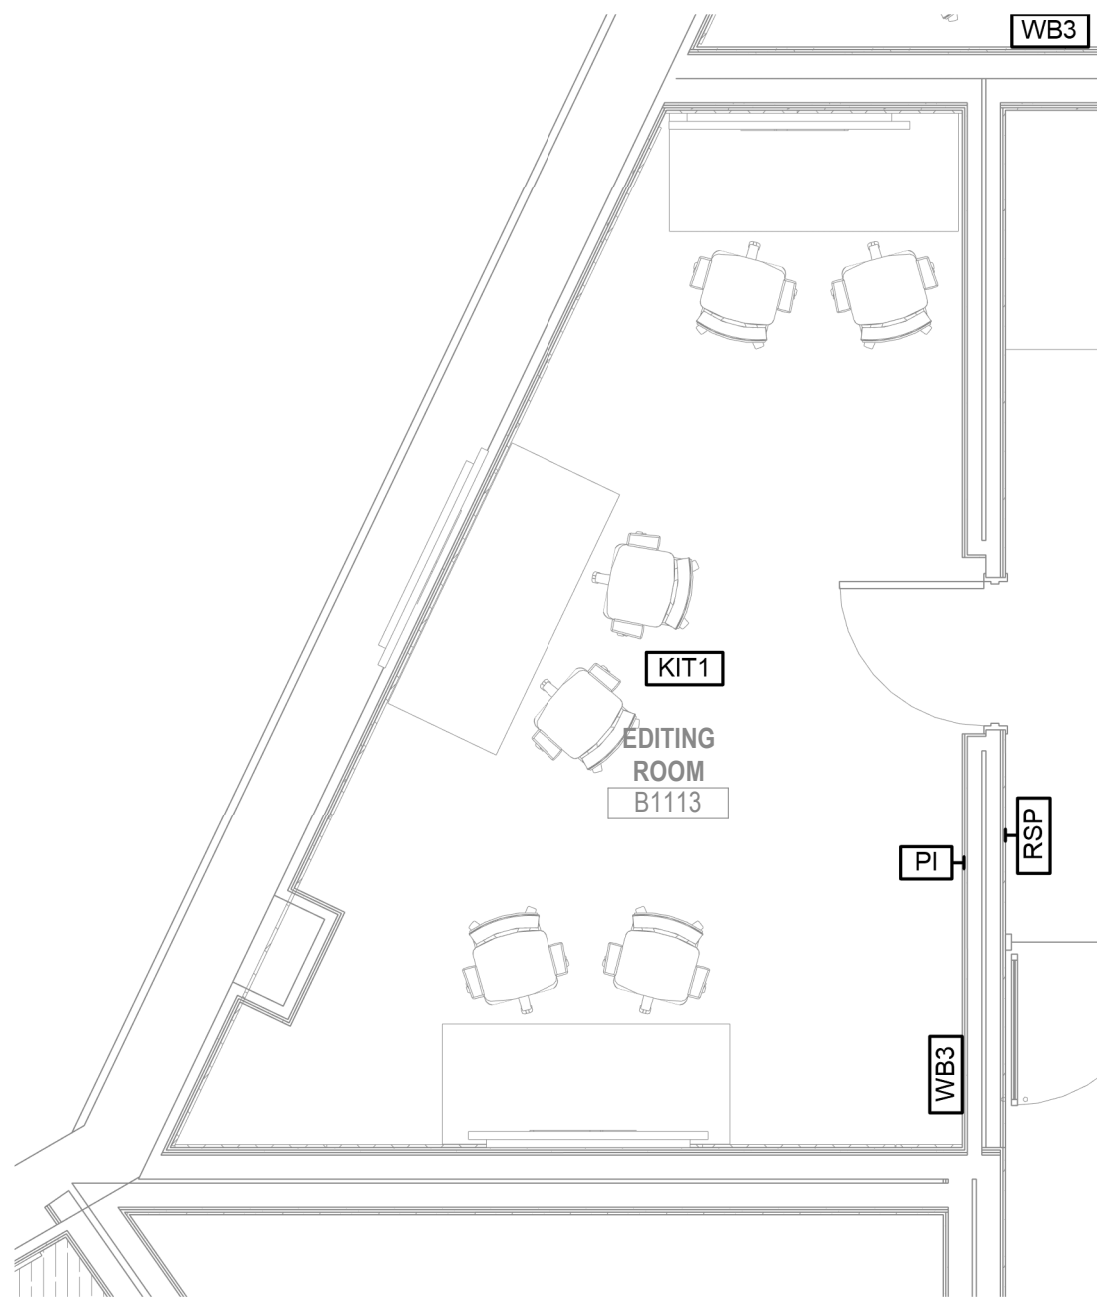


EDITING ROOM B1113 - ENLARGED PLAN - ADDITIVE BID
① ALTERNATE (RECORDING STUDIO)
1/4" = 1'-0"

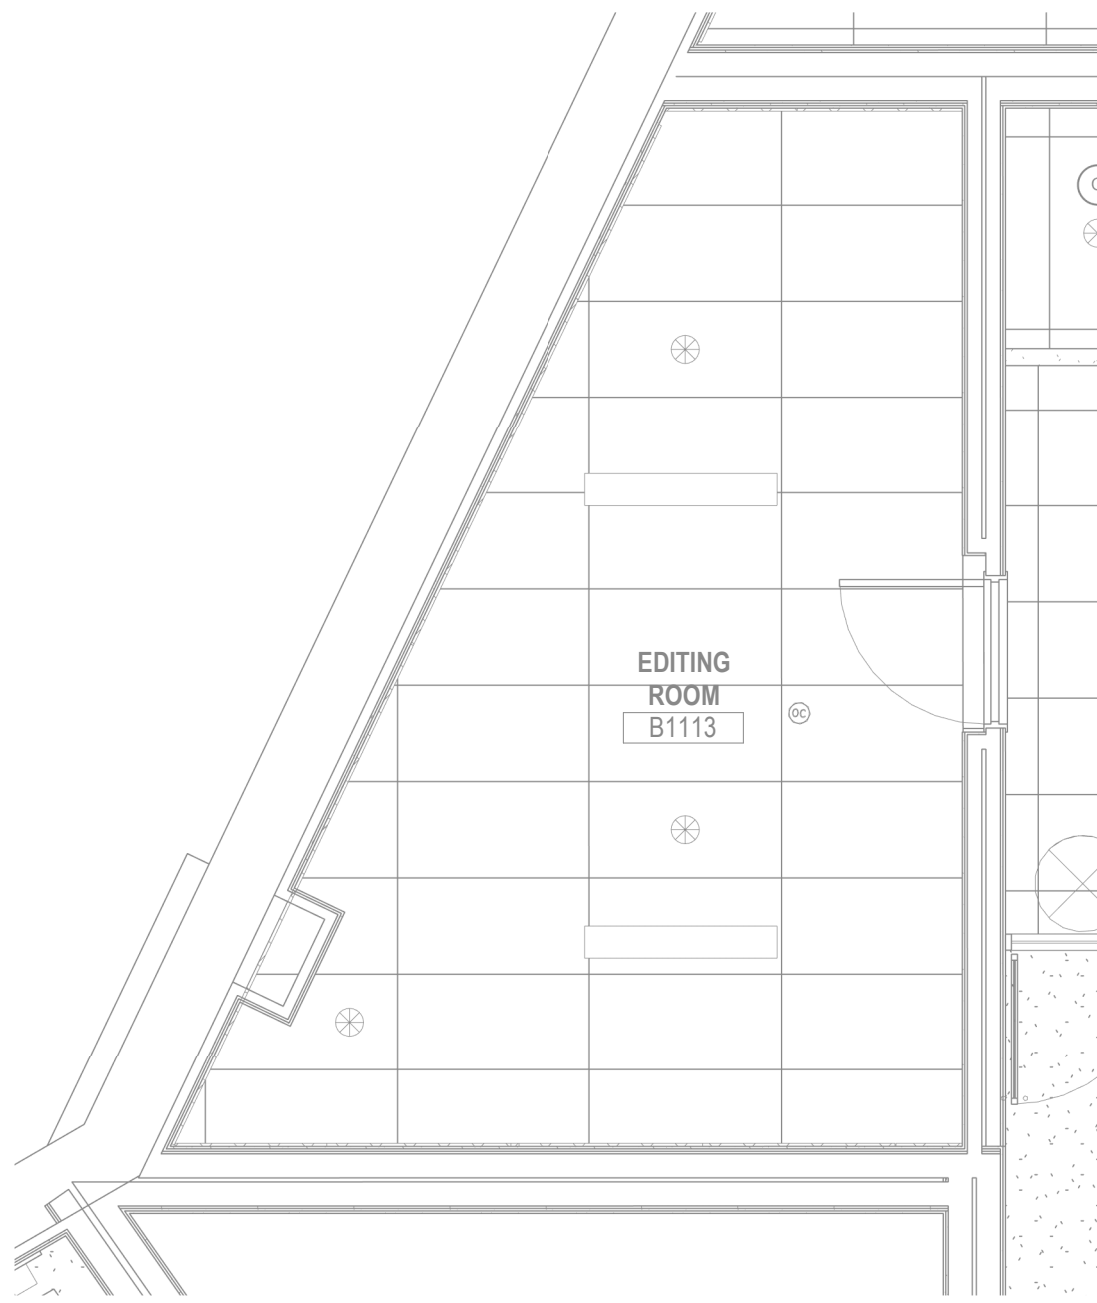


EDITING ROOM B1113 - ENLARGED RCP - ADDITIVE BID
② ALTERNATE (RECORDING STUDIO)
1/4" = 1'-0"

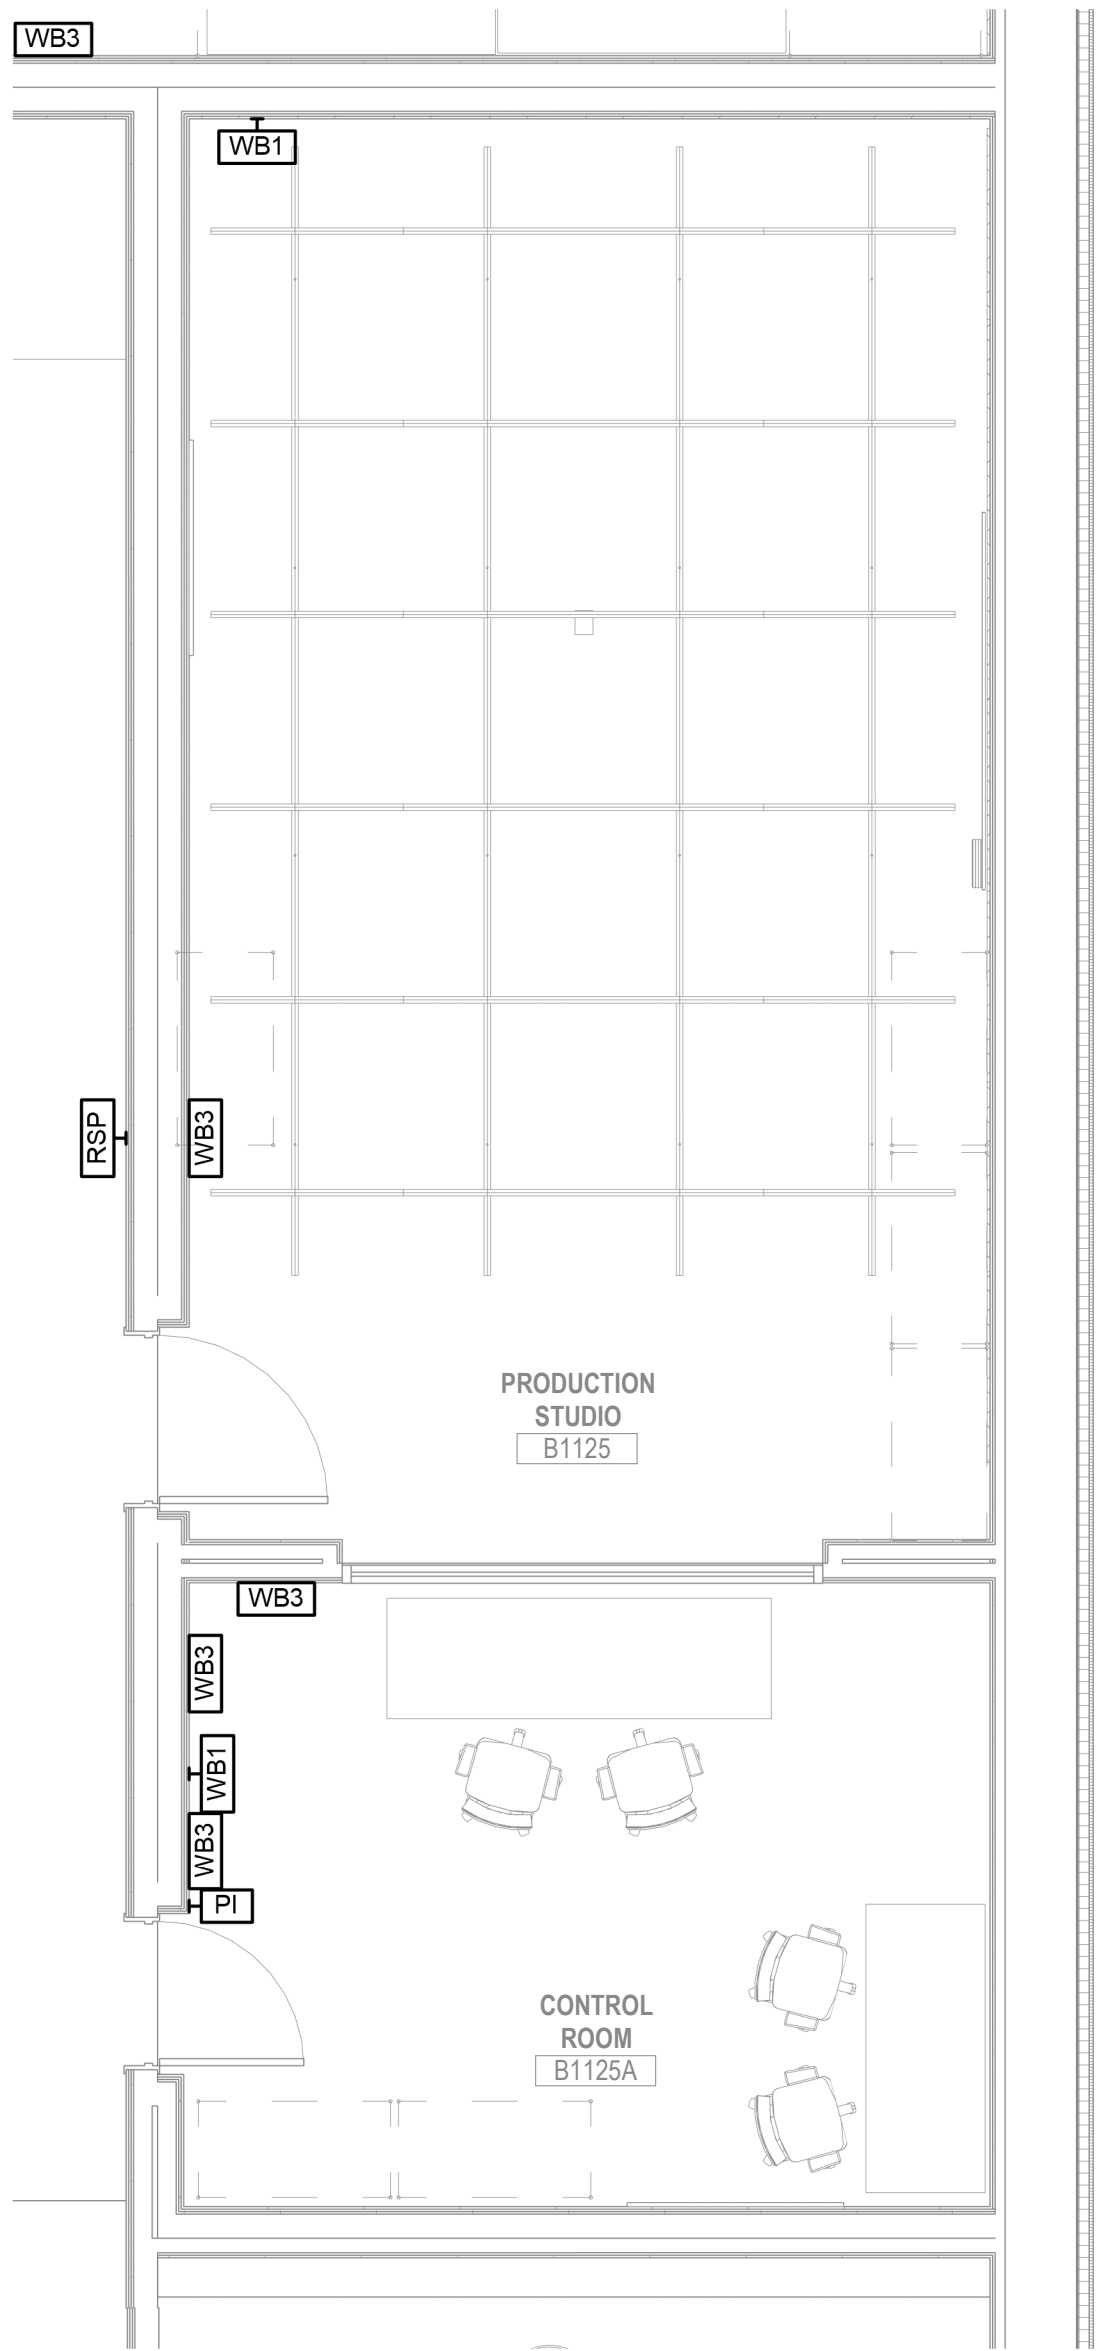

PRODUCTION STUDIO B1125 & CONTROL ROOM B1125A -
ENLARGED PLAN - ADDITIVE BID ALTERNATE (RECORDING
STUDIO)
③ 1/4" = 1'-0"

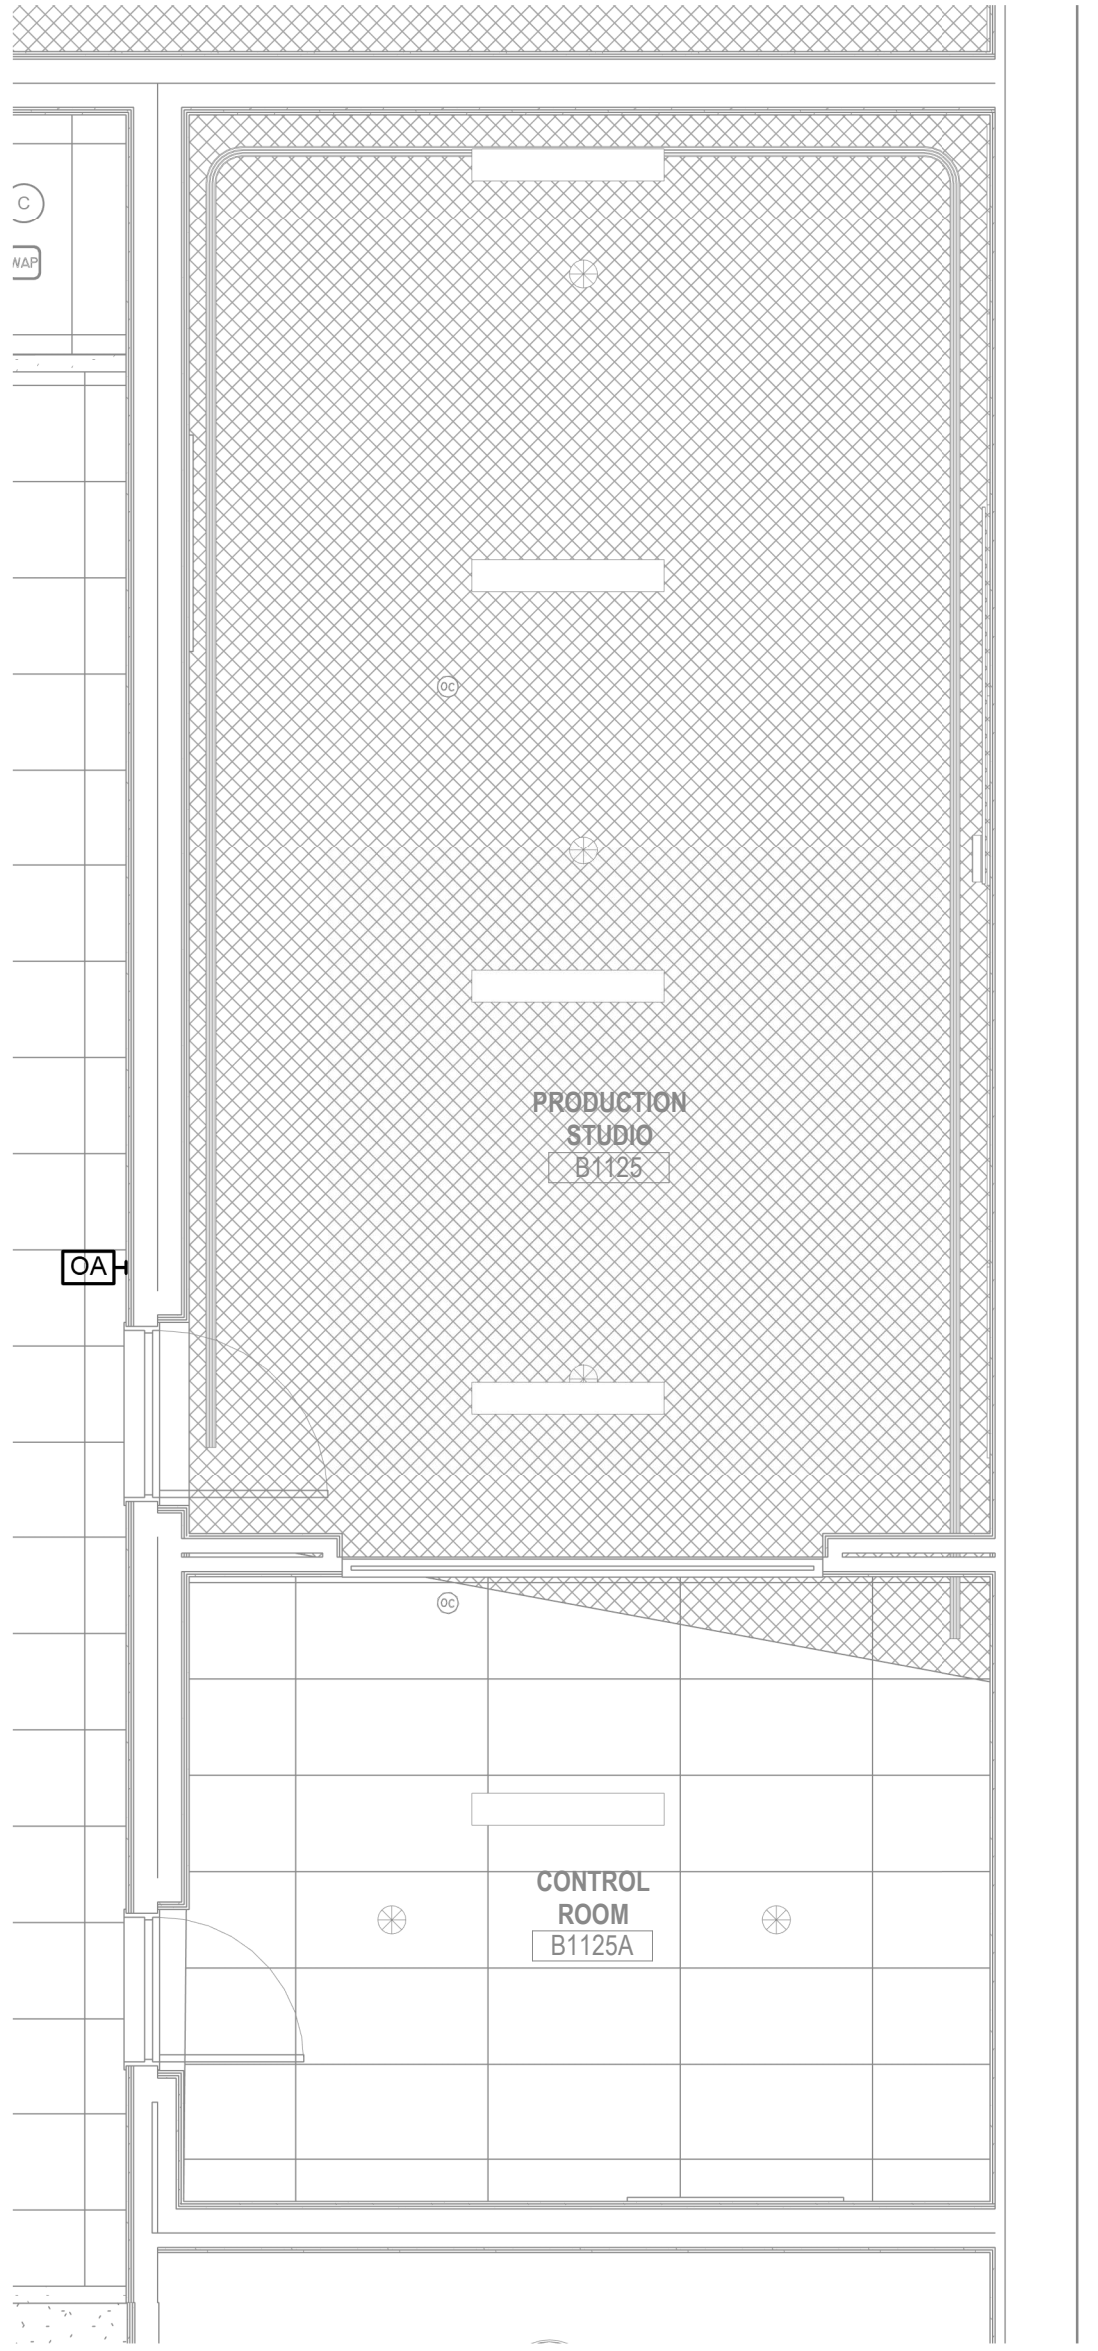

PRODUCTION STUDIO 1125 & CONTROL ROOM 1125A -
ENLARGED RCP - ADDITIVE BID ALTERNATE (RECORDING
STUDIO)
④ 1/4" = 1'-0"

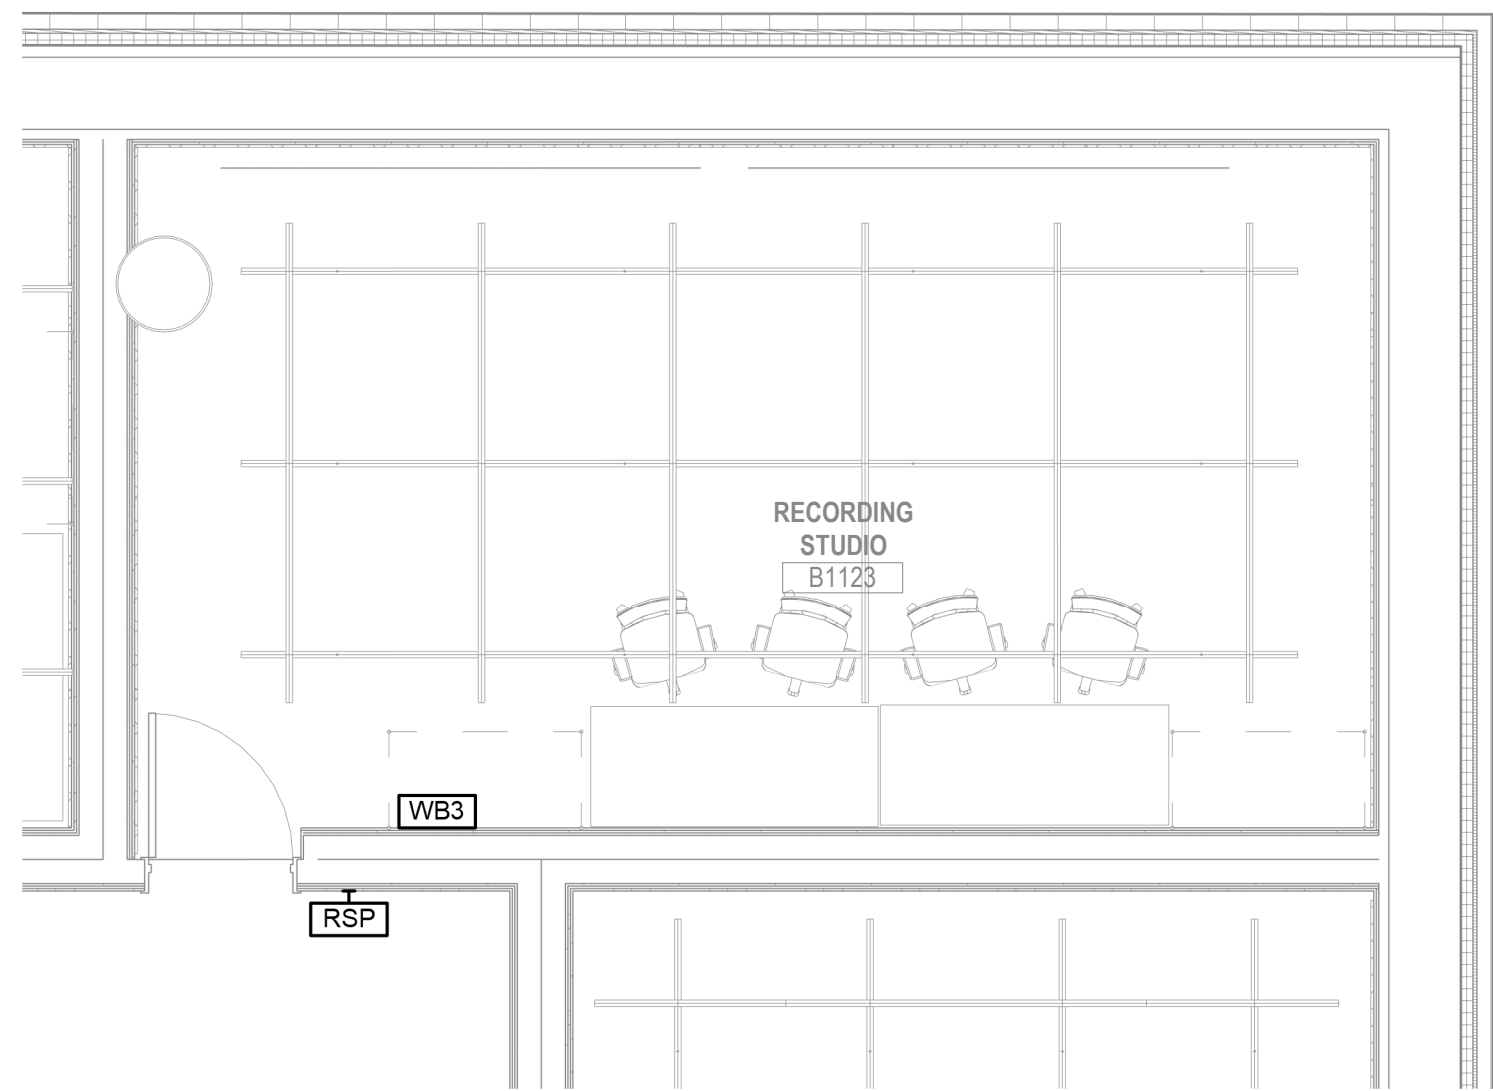

RECORDING STUDIO B1123 - ENLARGED PLAN - ADDITIVE
⑤ BID ALTERNATE (RECORDING STUDIO)
1/4" = 1'-0"



RECORDING STUDIO B1123 - ENLARGED RCP - ADDITIVE
⑥ BID ALTERNATE (RECORDING STUDIO)
1/4" = 1'-0"

KEYNOTES



UCB Gateway Building
Berkeley CA 94720

WEISS / MANFREDI + GENSLER

DESIGN ARCHITECT Weiss Manfredi 200 Hudson St. 10th Floor NY, NY 10013 United States Tel 212.760.9002 Tel 212.760.9002 Fax 212.760.9003	EXECUTIVE ARCHITECT Gensler 45 Fremont St., Suite 1500 San Francisco, CA 94105 United States Tel 415.433.3700 Fax 415.636.4599
STRUCTURAL ENGINEER MKA Interface Engineering 1301 Fifth Avenue Suite 3200 Seattle, WA 98101 United States Tel 206.292.1200 Fax xxx.xxx.xxxx	MEP ENGINEER TBD Consultants 135 Main Street, Suite 400 San Francisco, CA 94105 United States Tel 415.489.7240 Fax xxx.xxx.xxxx
CIVIL ENGINEER Shenwood Engineers 2548 Mission St. San Francisco, CA 94110 United States Tel 415.677.7300 Fax xxx.xxx.xxxx	COST ESTIMATING TBD Consultants 111 Pine St., Suite 1315 San Francisco, CA 94111 United States Tel 415.981.9430 Fax 415.981.9434
LIGHTING Auerbach Glasgow 1045 Sansome St., Suite 300 San Francisco, CA 94111 United States Tel 415.392.7528 Fax 415.392.7530	ACOUSTIC, SECURITY Shen, Misom, Wilke 351 California St., Suite 810 San Francisco, CA 94104 United States Tel 415.391.7610 Fax 415.391.0171
AV/IT SFM 351 Br. St. San Francisco, CA 94103 United States Tel 415.255.9140 Fax 415.255.9180	FOOD SERVICE Ciri - Little 335 Mission Street, 14th Floor San Francisco, CA 94105 United States Tel 415.922.9900 Fax xxx.xxx.xxxx
ELEVATOR Syska Hennessey 425 California St., Suite 400 San Francisco, CA 94104 United States Tel 415.288.9061 Fax xxx.xxx.xxxx	CODE/LIFE SAFETY Holmes Fire 235 Montgomery St., Suite 1250 San Francisco, CA 94104 United States Tel 415.693.1600 Fax xxx.xxx.xxxx
LANDSCAPE PGA Design 444 17th Street Oakland, CA 94612 United States Tel 510.465.1284 Fax 510.465.1286	DAT/LIGHTING L + U 1500 Ferry Point Alameda, CA 94501 P.O. Box 6146 Tel 510.521.3800 Fax 510.521.3520
BUILDING MAINTENANCE STCO 183A Beacon St South San Francisco, CA 94080 United States Tel 650.588.4626	ENVELOPE Henriques 101 Second Street, Suite 325 San Francisco, CA 94105 United States Tel 415.991.2000
WIND ENGINEERING RWI 203-1460 blvd de l'Innovation Bromont, Quebec J2L 0J8 Canada Tel 450.534.1007 Fax 519.623.1316	WATERPROOFING WUE 2000 Powell Street Suite 1650 Emeryville, CA 94608 Tel 510.428.2907
HARDWARE DCI 24072 San Juan Ave. Ste 212 Dana Point, CA, 92629 United States Tel 949.368.6571	ELECTRICAL (TRADE) CEI 1132 N 7th St San Jose, CA, 95112 United States Tel 408.898.9000
MECHANICAL (TRADE) ACCOCES 1133 Aladdin Ave San Leandro, CA, 94577 United States Tel 510.345.4300	PLUMBING (TRADE) Frank M Booth 251 Michelle Ct South SF, CA 94080 United States Tel 650.559.1844
FIRE PROTECTION (TRADE) Pibuss 523 Mayfair Ave South SF CA, 94080 United States Tel 650.588.2968	

△	Date	Description
	2022/05/18	UCB GATEWAY DESIGN DEVELOPMENT 100%
	2022/08/10	UCB GATEWAY CONSTRUCTION DOCS 95%
	2022/10/12	UCB GATEWAY CONSTRUCTION DOCS 95%
	2022/12/02	UCB GATEWAY CONSTRUCTION DOCS 100%
	2023/03/29	PERMIT PLAN CHECK #3

Seal / Signature

DATE 03/24/23
RAY ENWEZHER
REG. NO. 90911
EXPIRES 12/31/2025

Project Name
UCB Gateway


Project Number
01.4968.000

Description
AUDIOVISUAL ENLARGED PLANS,
RCP & ELEVATIONS


Scale
1/4" = 1'-0"

TA5.003


3/27/2023 9:53:04 AM B:\1305\107\4968.00 - UCB Gateway\Technology - 01\4968.00 - UCB Gateway.rvt

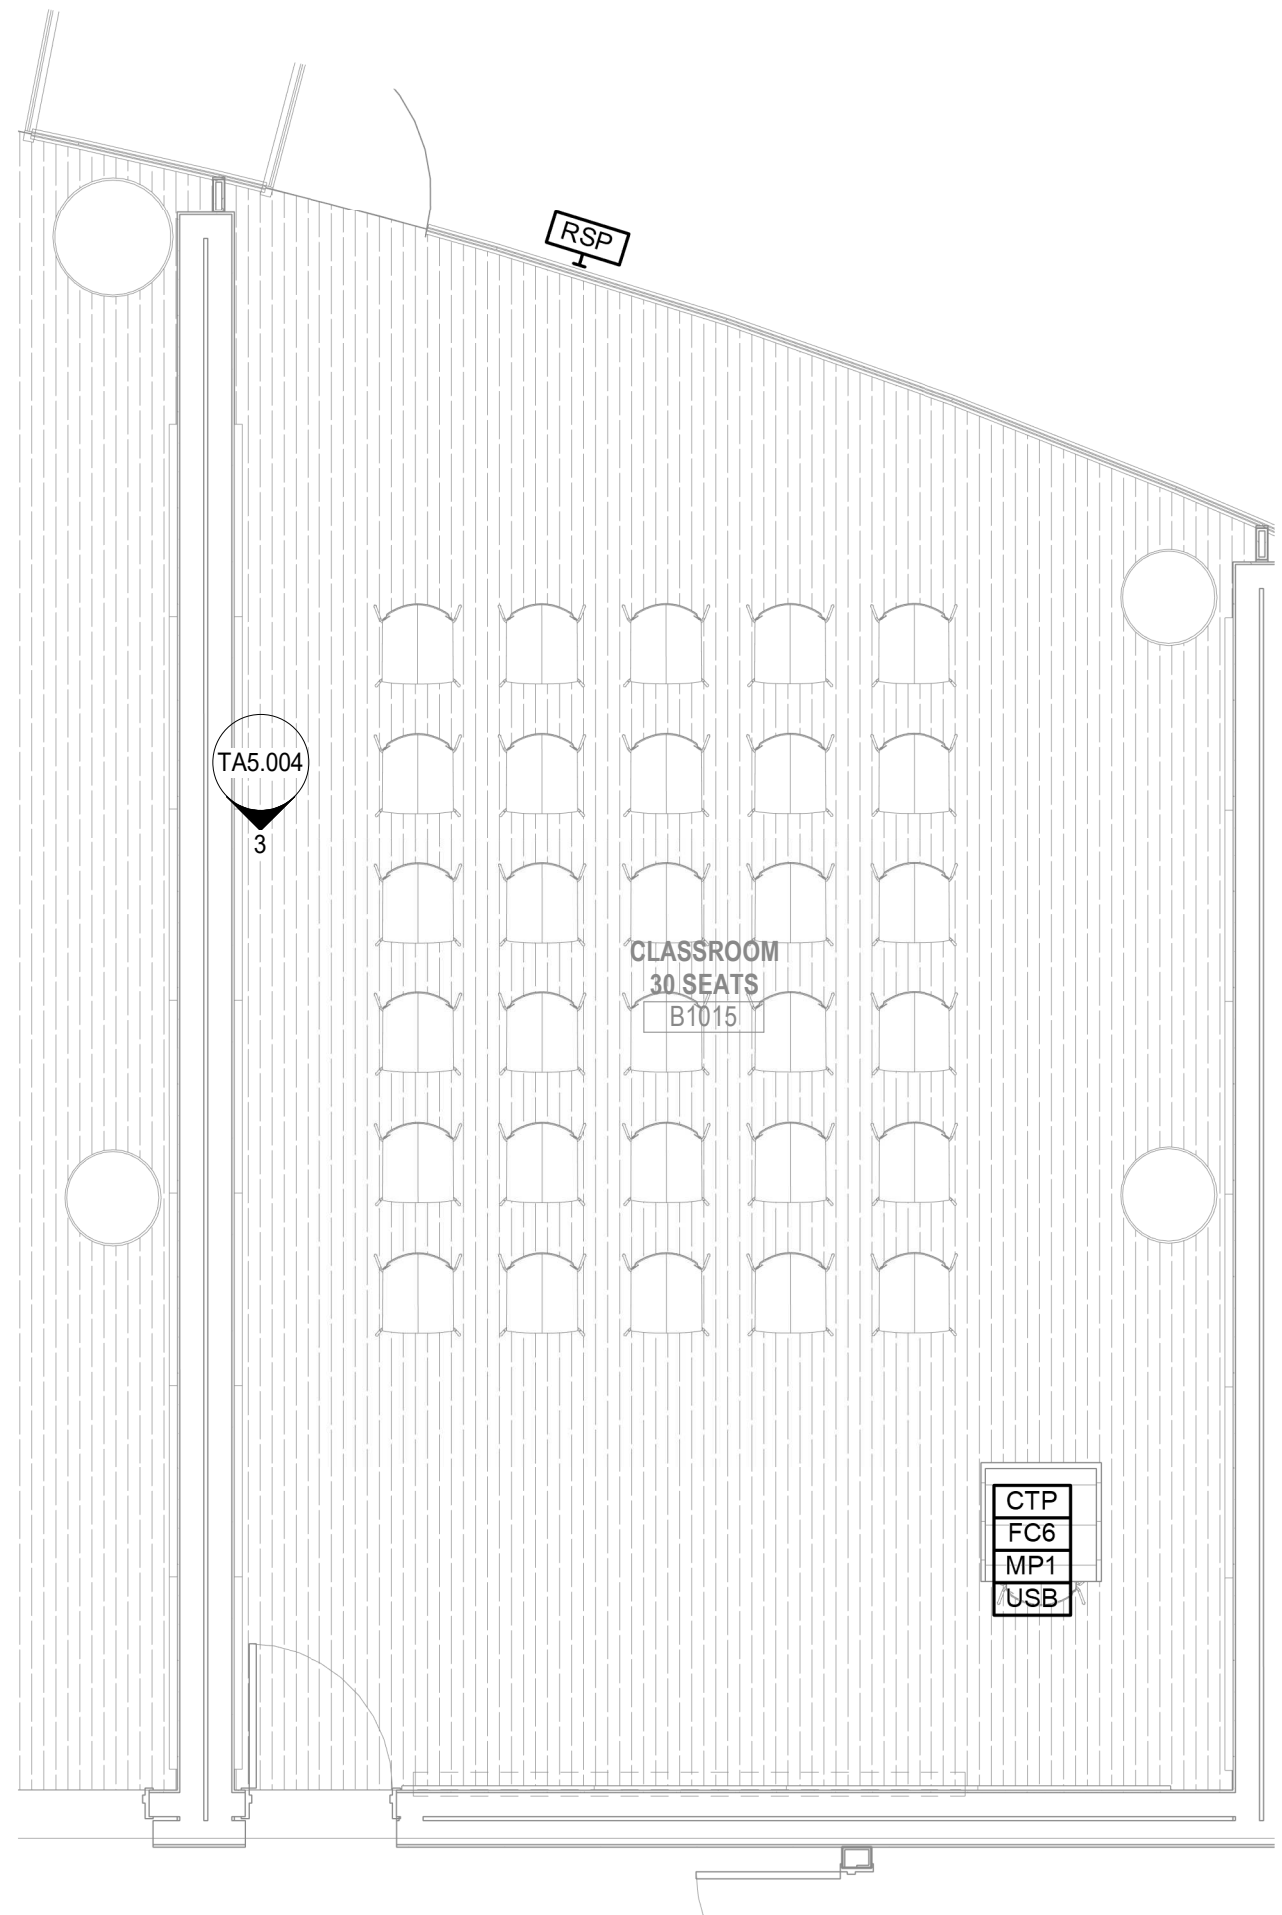


1 CLASSROOM 30 SEATS B1015 - ENLARGED PLAN
1/4" = 1'-0"

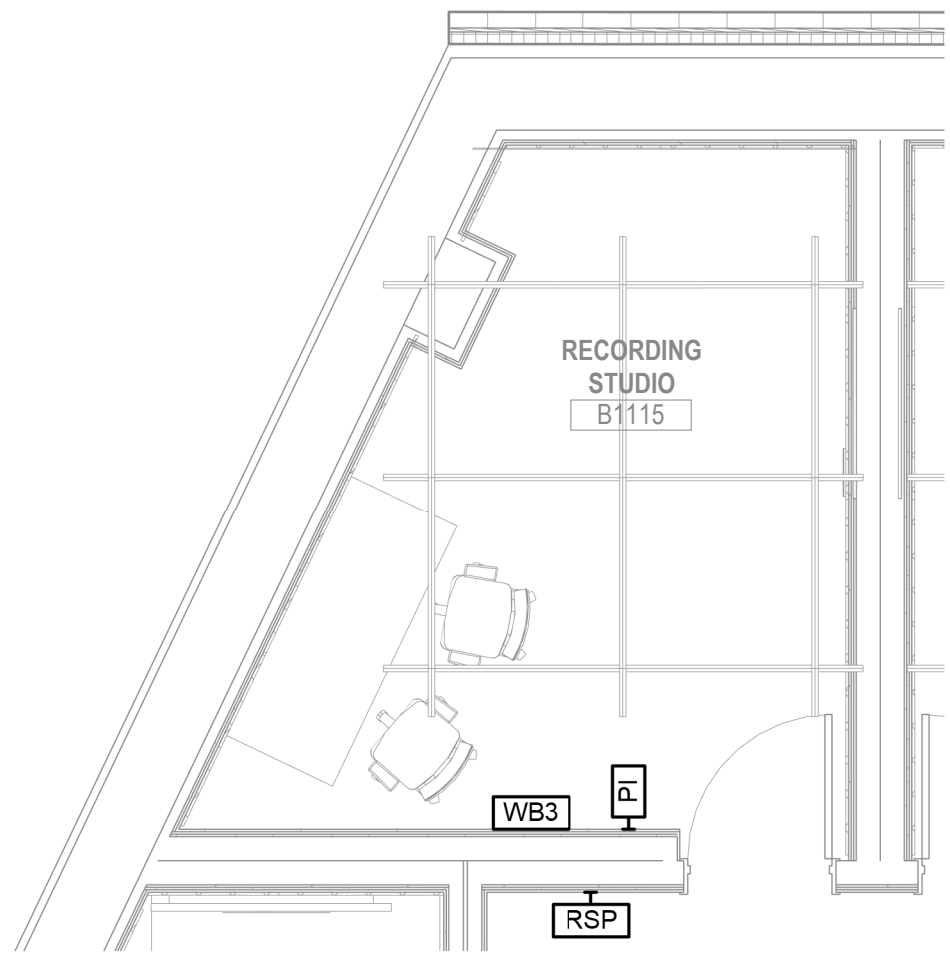


4 RECORDING STUDIO B1115 - ENLARGED PLAN - ADDITIVE
BID ALTERNATE (RECORDING STUDIO)
1/4" = 1'-0"

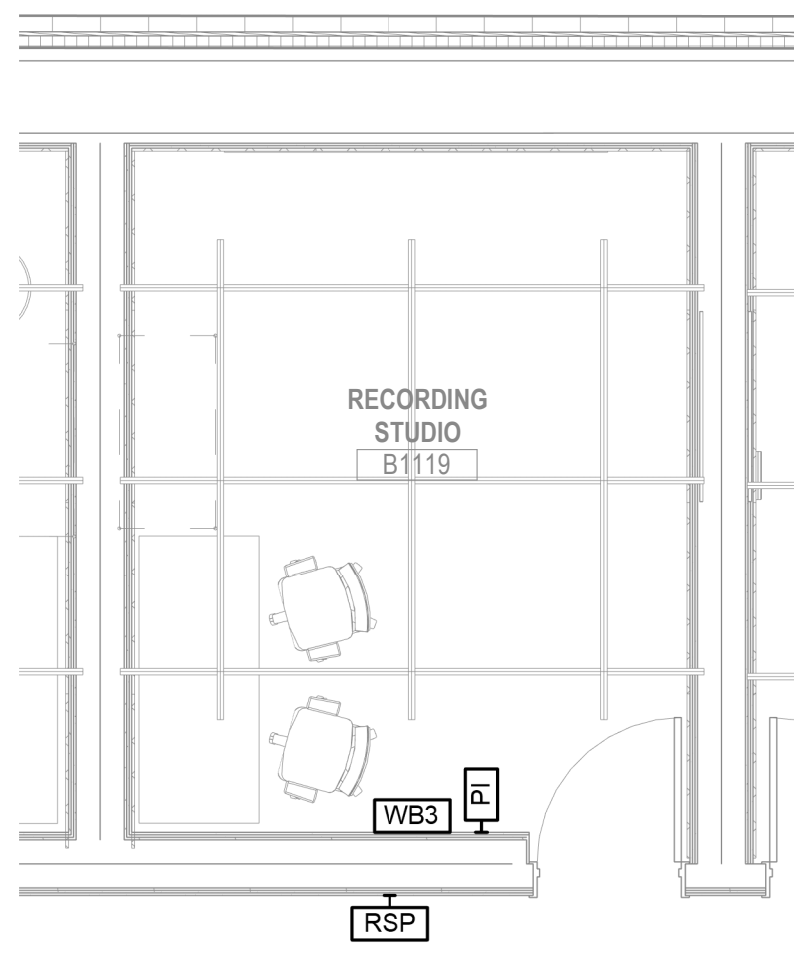


6 RECORDING STUDIO B1119 - ENLARGED PLAN - ADDITIVE
BID ALTERNATE (RECORDING STUDIO)
1/4" = 1'-0"

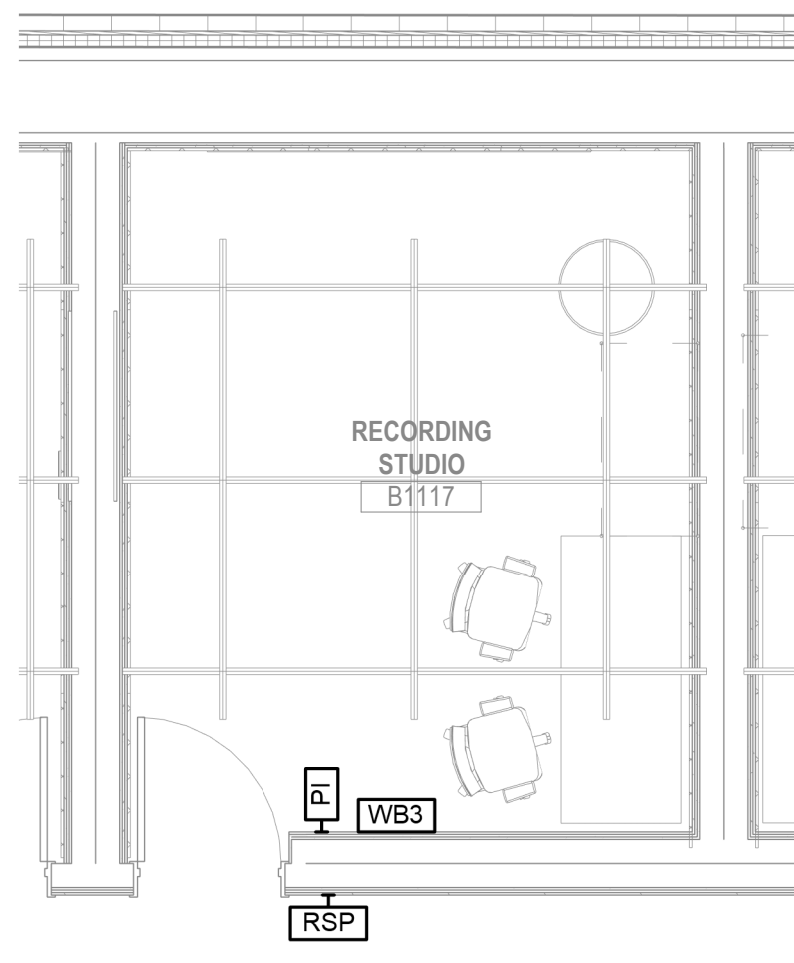


8 RECORDING STUDIO B1117 - ENLARGED PLAN - ADDITIVE
BID ALTERNATE (RECORDING STUDIO)
1/4" = 1'-0"

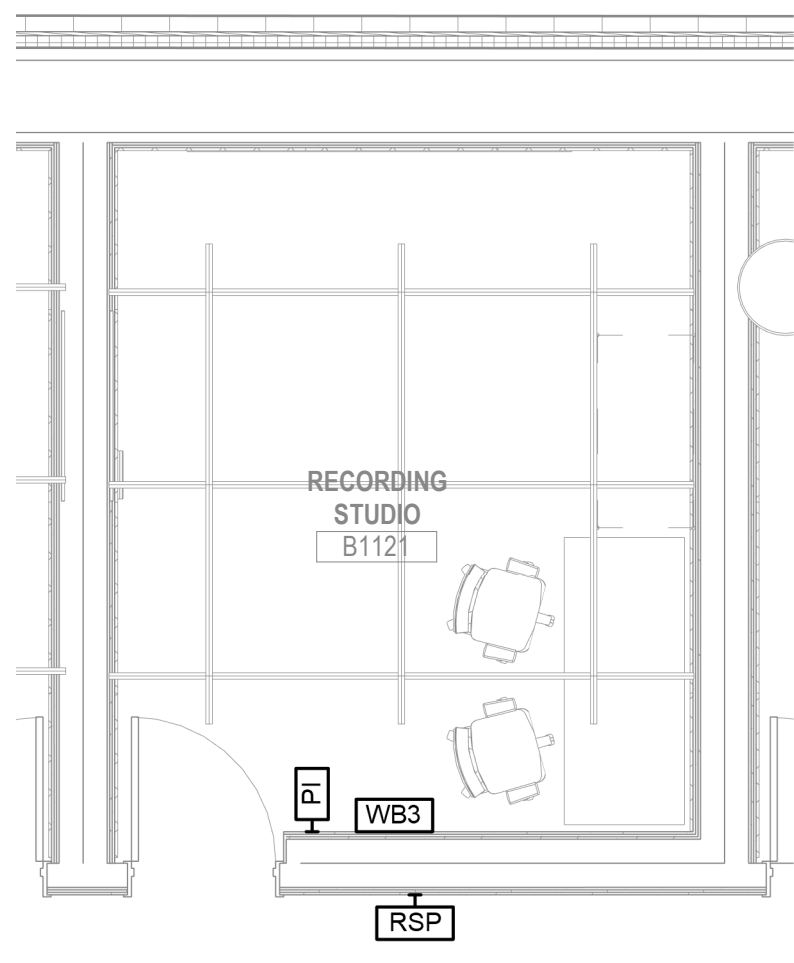


10 RECORDING STUDIO B1121 - ENLARGED PLAN - ADDITIVE
BID ALTERNATE (RECORDING STUDIO)
1/4" = 1'-0"

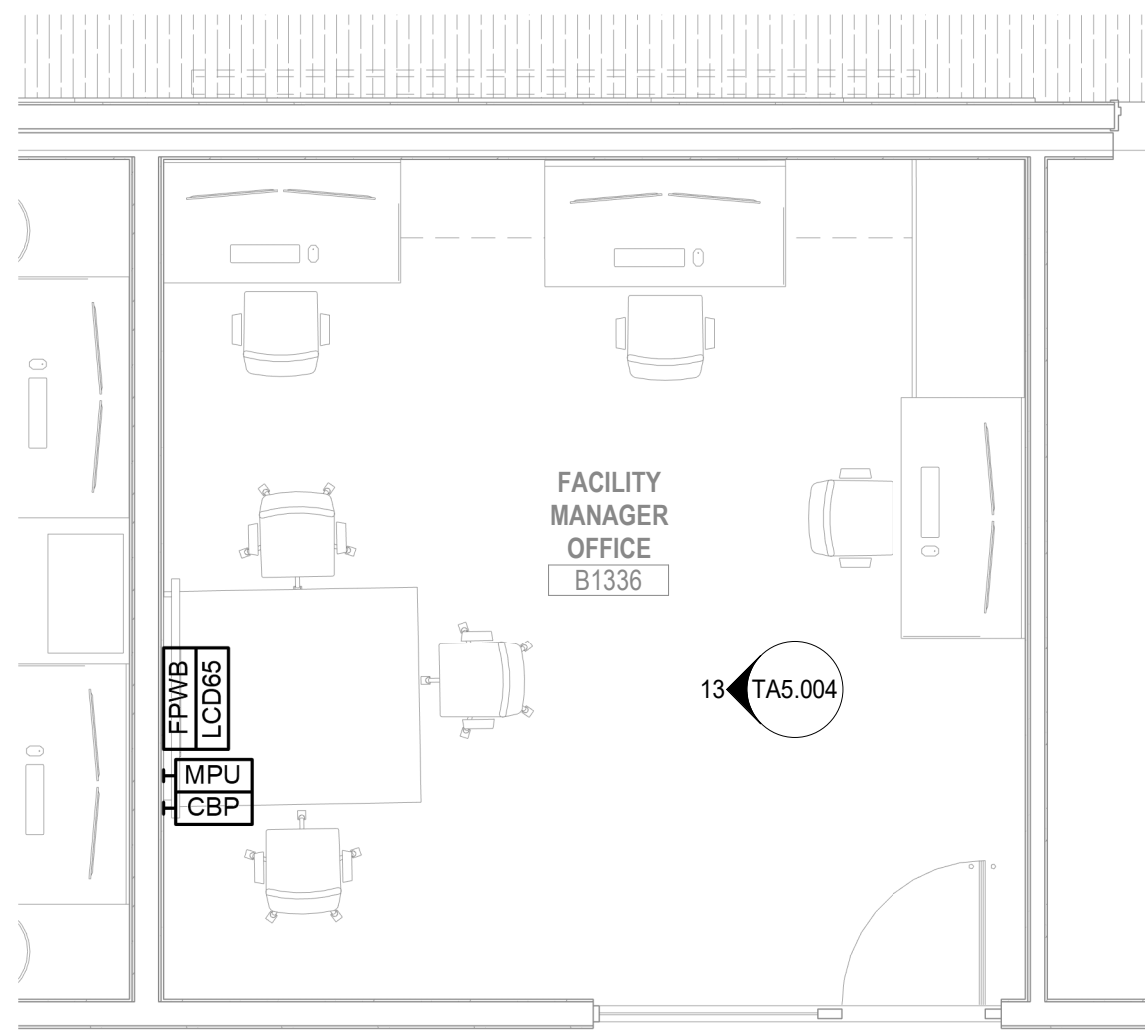


12 FACILITY MANAGER OFFICE B1336 - ENLARGED PLAN
1/4" = 1'-0"

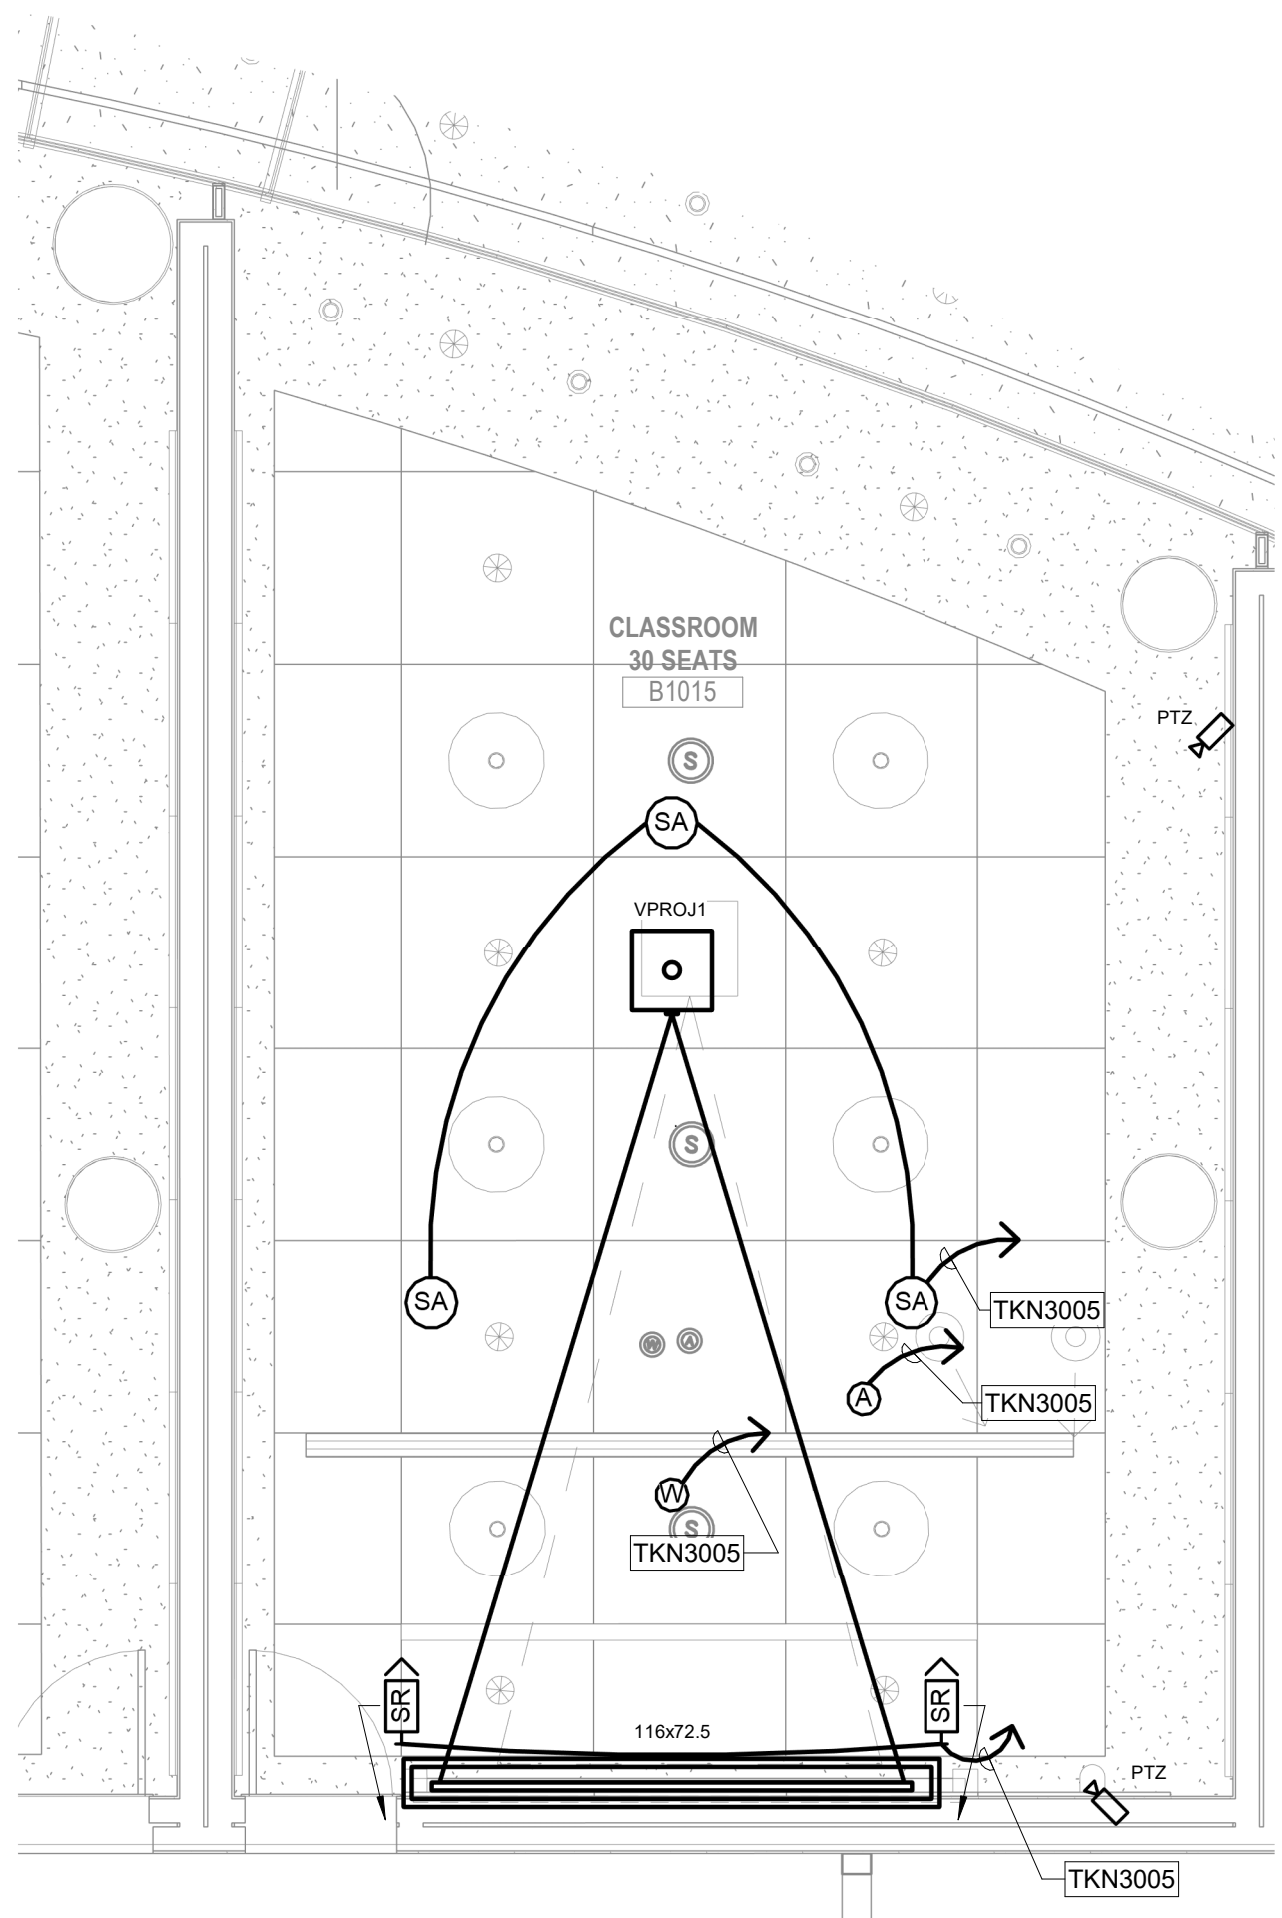


2 CLASSROOM 30 SEATS B1015 - ENLARGED RCP
1/4" = 1'-0"

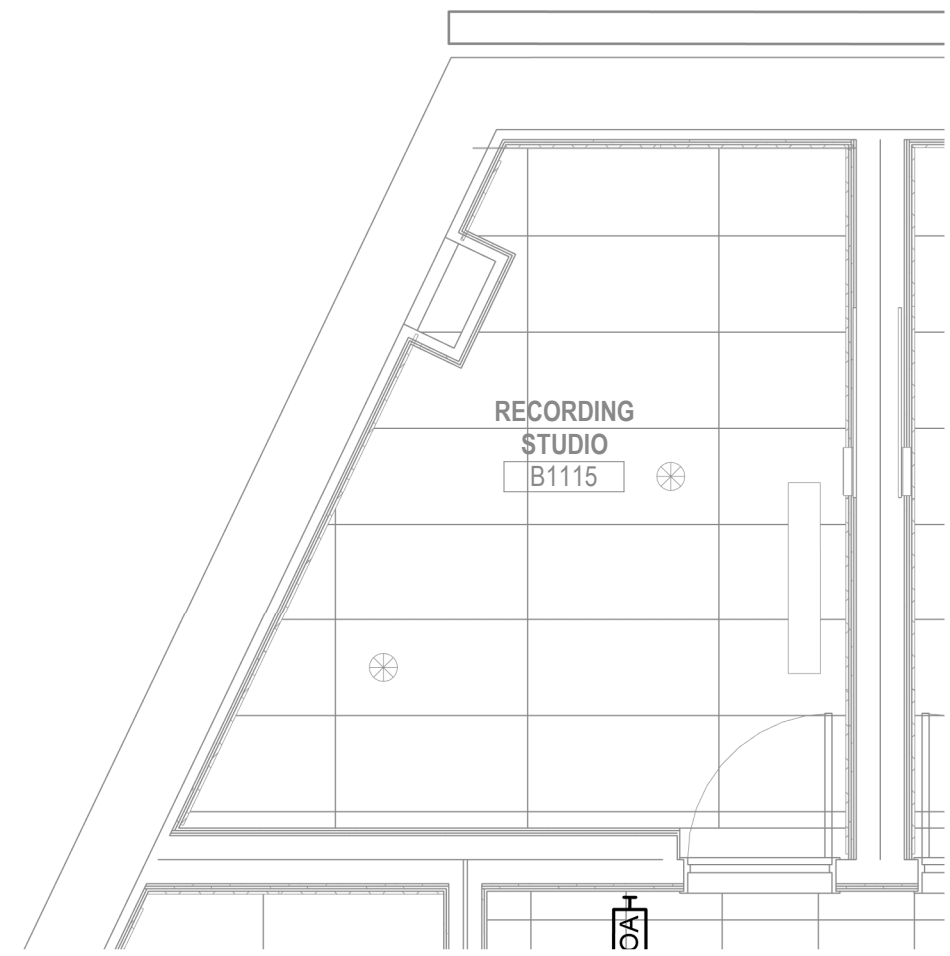


5 RECORDING STUDIO B1115 - ENLARGED RCP - ADDITIVE
BID ALTERNATE (RECORDING STUDIO)
1/4" = 1'-0"

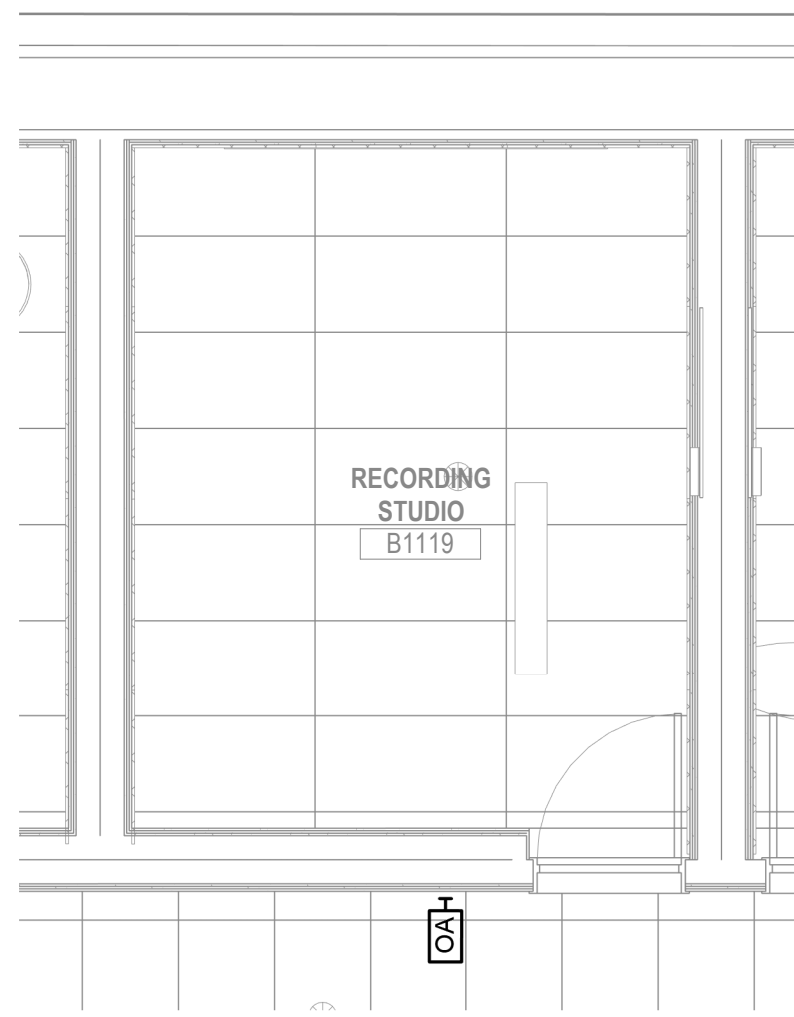


7 RECORDING STUDIO B1119 - ENLARGED RCP - ADDITIVE
BID ALTERNATE (RECORDING STUDIO)
1/4" = 1'-0"

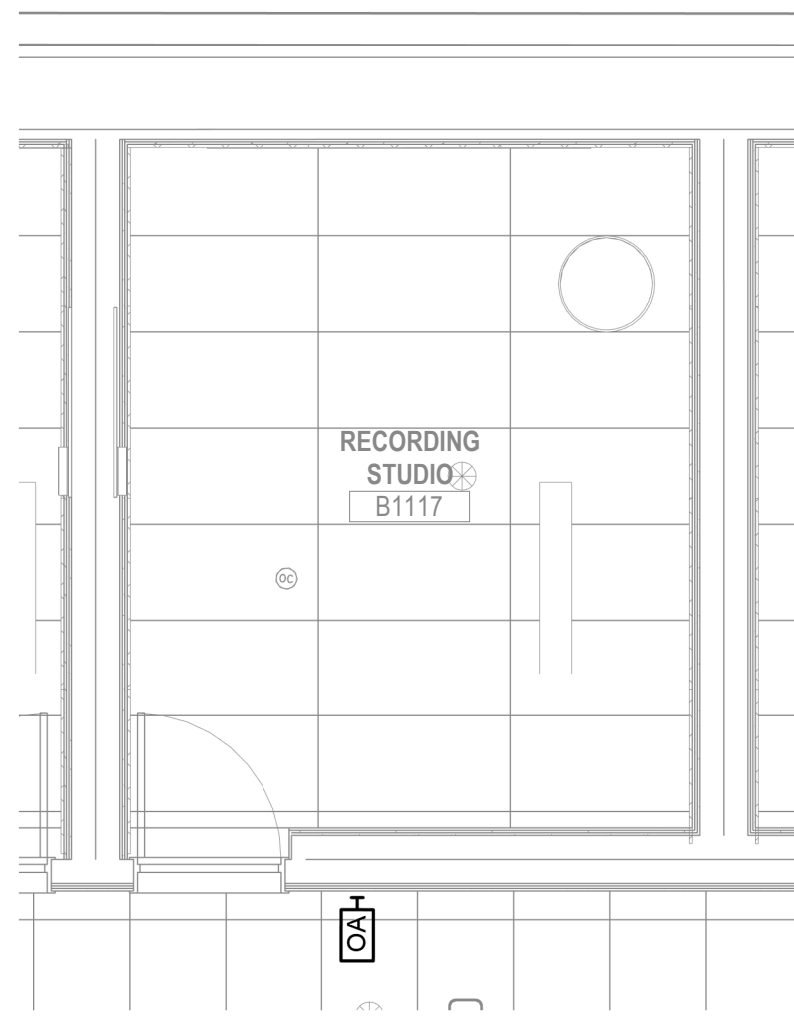


9 RECORDING STUDIO B1117 - ENLARGED RCP - ADDITIVE
BID ALTERNATE (RECORDING STUDIO)
1/4" = 1'-0"

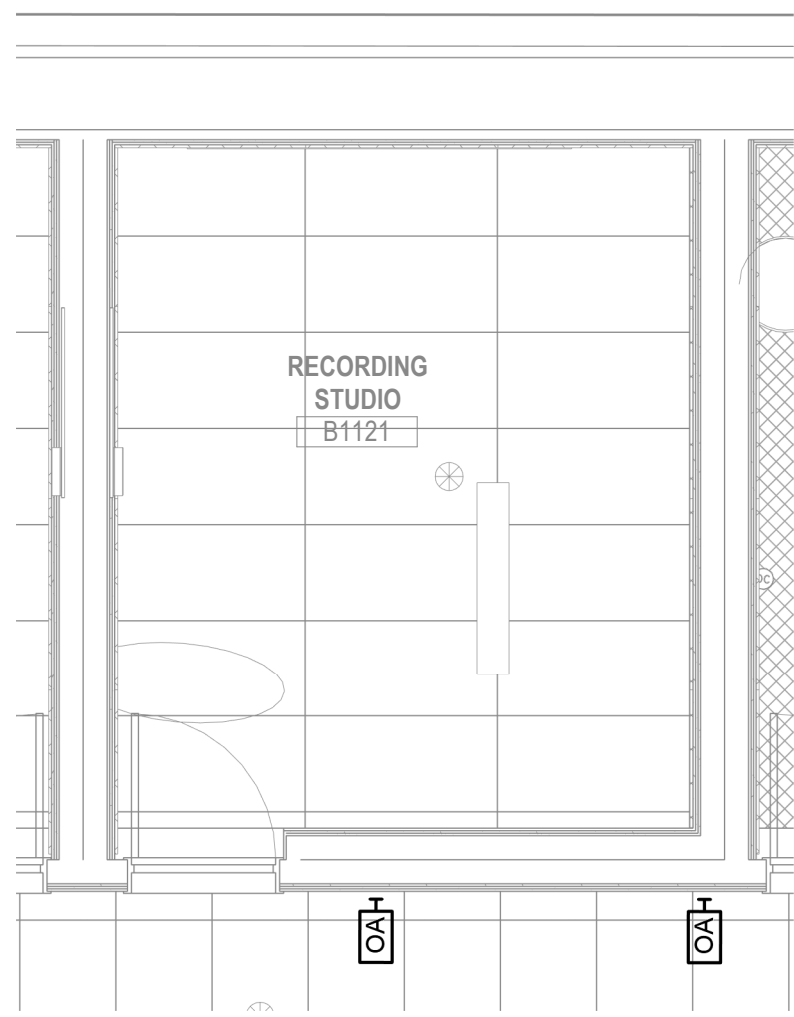

11 RECORDING STUDIO B1121 - ENLARGED RCP - ADDITIVE
BID ALTERNATE (RECORDING STUDIO)
1/4" = 1'-0"

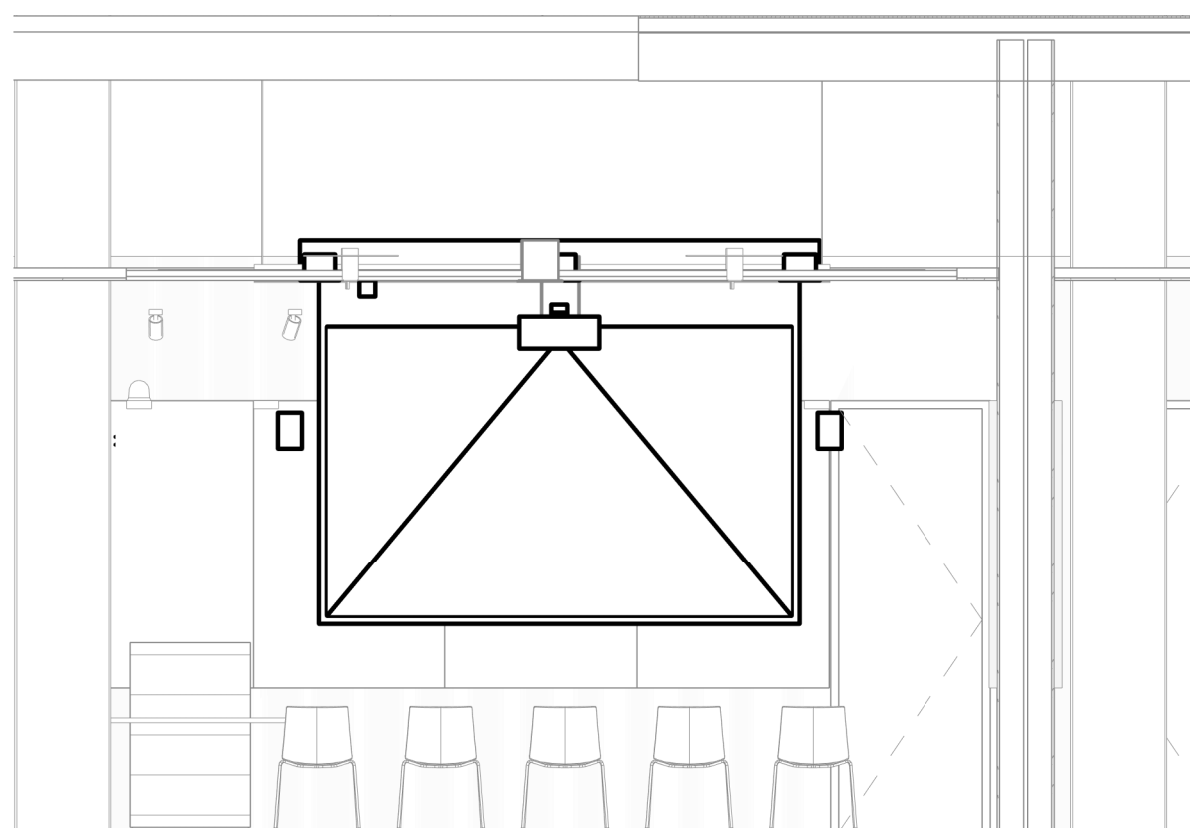

3 CLASSROOM 30 SEATS B1015 - SOUTH ELEVATION
1/4" = 1'-0"

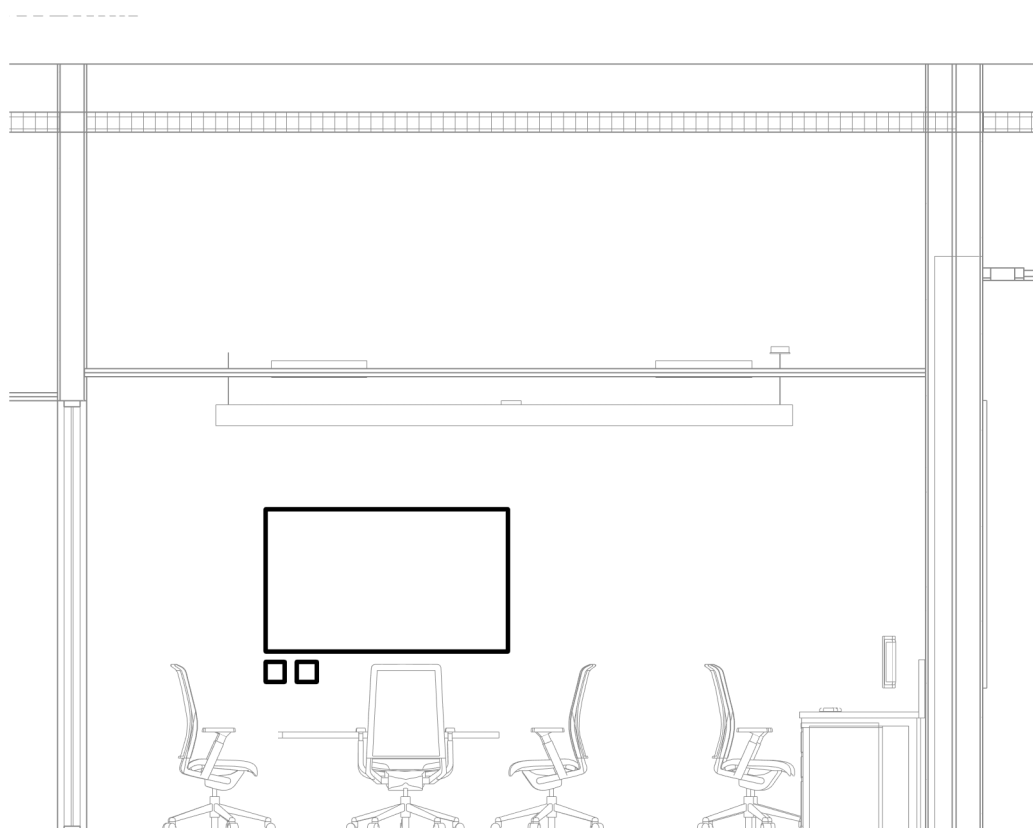

13 FACILITY MANAGER OFFICE B1336 - WEST ELEVATION
1/4" = 1'-0"

KEYNOTES	
TKN3005	H.R. TO AV IDF B1040B



UCB Gateway Building
Berkeley CA 94720

WEISS / MANFREDI + GENSLER

DESIGN ARCHITECT
Weiss Manfredi
200 Hudson St. 10th Floor
NY, NY 10013
United States
Tel 212.760.9002
Fax 212.760.9003

EXECUTIVE ARCHITECT
Gensler
45 Fremont St., Suite 1500
San Francisco, CA 94105
United States
Tel 415.433.3700
Fax 415.636.4599

STRUCTURAL ENGINEER
MKA
1301 Fifth Avenue Suite 3200
Seattle, WA 98101
United States
Tel 206.292.1200
Fax xxx.xxx.xxxx

MEP ENGINEER
Interface Engineering
135 Main Street, Suite 400
San Francisco, CA 94105
United States
Tel 415.489.7240
Fax xxx.xxx.xxxx

CIVIL ENGINEER
Shenwood Engineers
2548 Mission St.
San Francisco, CA 94110
United States
Tel 415.677.7300
Fax xxx.xxx.xxxx

COST ESTIMATING
TBD Consultants
111 Pine St., Suite 1315
San Francisco, CA 94111
United States
Tel 415.392.7310
Fax 415.981.9434

ACUSTIC, SECURITY
Shen, Misom, Wilke
351 California St., Suite 810
San Francisco, CA 94104
United States
Tel 415.392.7310
Fax 415.391.0171

AVIT
SFM
351 Br. St.
San Francisco, CA 94103
United States
Tel 415.252.9140
Fax 415.255.9180

FOOD SERVICE
Ciri - Little
335 Mission Street, 14th Floor
San Francisco, CA 94105
United States
Tel 415.392.9200
Fax xxx.xxx.xxxx

ELEVATOR
Syska Hennessy
425 California St., Suite 400
San Francisco, CA 94104
United States
Tel 415.288.9061
Fax xxx.xxx.xxxx

CODE/LIFE SAFETY
Holmes Fire
235 Montgomery St., Suite 1250
San Francisco, CA 94104
United States
Tel 415.393.1600
Fax xxx.xxx.xxxx

LANDSCAPE
PGA Design
444 17th Street
Oakland, CA 94612
United States
Tel 510.465.1284
Fax 510.465.1286

BUILDING MAINTENANCE
SITCO
183A Beacon St
South San Francisco, CA 94080
United States
Tel 650.588.4626

WIND ENGINEERING
RWI
203-1460 Blvd de l'Innovation
Bromont, Quebec J2L 0J8
Canada
Tel 450.534.1007
Fax 519.623.1316

WATERPROOFING
WUE
2000 Powell Street
Suite 1650
Emeryville, CA 94608
Tel 510.428.2907

HARDWARE
DCI
24672 San Juan Ave. Ste 212
Dana Point, CA, 92629
United States
Tel 949.368.6571

ELECTRICAL (TRADE)
CEI
1132 N 7th St
San Jose, CA, 95112
United States
Tel 408.898.9000

MECHANICAL (TRADE)
ACCDES
1133 Aladdin Ave
San Leandro, CA, 94577
United States
Tel 510.346.4300

PLUMBING (TRADE)
Frank M Booth
251 Nicholas Ct
South SF, CA, 94080
United States
Tel 650.359.1844

FIRE PROTECTION (TRADE)
Pribuss
523 Mayfair Ave
South SF CA, 94080
United States
Tel 650.588.2968

Seal / Signature

DATE 03/24/23
RAY ENWICHES
REG. NO. 106011
EXPIRES 12/31/2025

Project Name
UCB Gateway

Project Number
01.4968.000

Description
AUDIOVISUAL ENLARGED PLANS,
RCP & ELEVATIONS

Scale
1/4" = 1'-0"

TA5.004



COMMUNICATIONS PLAN - LOWER LEVEL - ADDITIVE BID
① ALTERNATE (RECORDING STUDIO)
1/8" = 1'-0"



COMMUNICATIONS RCP - LOWER LEVEL - ADDITIVE BID
② ALTERNATE (RECORDING STUDIO)
1/8" = 1'-0"




UCB Gateway Building
Berkeley CA 94720

WEISS / MANFREDI + GENSLER

DESIGN ARCHITECT Weiss Manfredi 200 Hudson St. 10th Floor NY, NY 10013 United States Tel 212.760.9002 Fax 212.760.9003	EXECUTIVE ARCHITECT Gender 45 Fremont St., Suite 1500 San Francisco, CA 94105 United States Tel 415.433.3700 Fax 415.636.4599
STRUCTURAL ENGINEER MKA Interface Engineering 1301 Fifth Avenue Suite 3200 Seattle, WA 98101 United States Tel 206.292.1200 Fax xxx.xxx.xxxx	MEP ENGINEER Shenwood Engineers 2548 Mission St. San Francisco, CA 94110 United States Tel 415.677.7300 Fax xxx.xxx.xxxx
CIVIL ENGINEER Shenwood Engineers 2548 Mission St. San Francisco, CA 94110 United States Tel 415.677.7300 Fax xxx.xxx.xxxx	COST ESTIMATING TBD Consultants 111 Pine St., Suite 1315 San Francisco, CA 94111 United States Tel 415.391.7510 Fax 415.981.9434
LIGHTING Auerbach Glasgow 1045 Sansome St., Suite 300 San Francisco, CA 94111 United States Tel 415.392.7328 Fax 415.392.7330	ACOUSTIC, SECURITY Shen, Misson, Wilke 351 California St., Suite 810 San Francisco, CA 94104 United States Tel 415.391.0171 Fax 415.391.0171
AVIT SFM 351 Br. St. San Francisco, CA 94103 United States Tel 415.255.9140 Fax 415.255.9180	FOOD SERVICE Cris - Little 335 Mission Street, 14th Floor San Francisco, CA 94105 United States Tel 415.392.3900 Fax xxx.xxx.xxxx
ELEVATOR Syska Hennessey 425 California St., Suite 400 San Francisco, CA 94104 United States Tel 415.288.9061 Fax xxx.xxx.xxxx	CODE/LIFE SAFETY Holmes Fire 235 Montgomery St., Suite 1250 San Francisco, CA 94104 United States Tel 415.393.1600 Fax xxx.xxx.xxxx
LANDSCAPE PGA Design 444 17th Street Oakland, CA 94612 United States Tel 510.465.1284 Fax 510.465.1286	DAYLIGHTING L + U 1500 Ferry Point Alameda, CA 94501 P.O. Box 6146 Tel 510.521.3800 Fax 510.521.3520
BUILDING MAINTENANCE STICO 183A Beacon St South San Francisco, CA 94080 United States Tel 650.588.4626	ENVELOPE Herriges 101 Second Street, Suite 325 San Francisco, CA 94105 United States Tel 415.991.2000
WIND ENGINEERING RWI 203-1460 Blvd de l'Innovation Bromont, Quebec J2L 0J8 Canada Tel 450.534.1007 Fax 519.623.1316	WATERPROOFING WUE 2000 Powell Street Suite 1650 Emeryville, CA 94608 Tel 510.428.2907
HARDWARE DCI 24072 San Juan Ave. Ste 212 Dana Point, CA, 92629 United States Tel 949.368.6571	ELECTRICAL (TRADE) CEI 1132 N 7th St San Jose, CA, 95112 United States Tel 408.898.8000
MECHANICAL (TRADE) ACCDES 1133 Alameda Ave San Leandro, CA, 94577 United States Tel 510.346.4300	PLUMBING (TRADE) Frank M Booth 251 Michelle Ct South SF, CA 94080 United States Tel 510.346.4300
FIRE PROTECTION (TRADE) Pibuss 523 Mayfair Ave South SF CA, 94080 United States Tel 650.588.2968	

△	Date	Description
	2022/05/18	UCB GATEWAY DESIGN DEVELOPMENT 100%
	2022/08/10	UCB GATEWAY CONSTRUCTION DOCS 50%
	2022/10/12	UCB GATEWAY CONSTRUCTION DOCS 95%
	2022/12/02	UCB GATEWAY CONSTRUCTION DOCS 100%
	2023/03/29	PERMIT PLAN CHECK #3

Seal / Signature

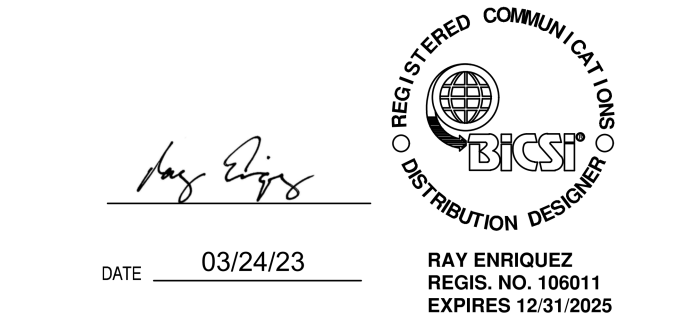
DATE 03/24/23
RAY ENRIQUEZ
REG. NO. 106011
EXPIRES 12/31/2025

Project Name
UCB Gateway

Project Number
01.4968.000

Description
COMMUNICATIONS PLAN & RCP -
LOWER LEVEL - ADDITIVE BID
ALTERNATE (RECORDING STUDIO)

Scale
1/8" = 1'-0"

TN5.601