


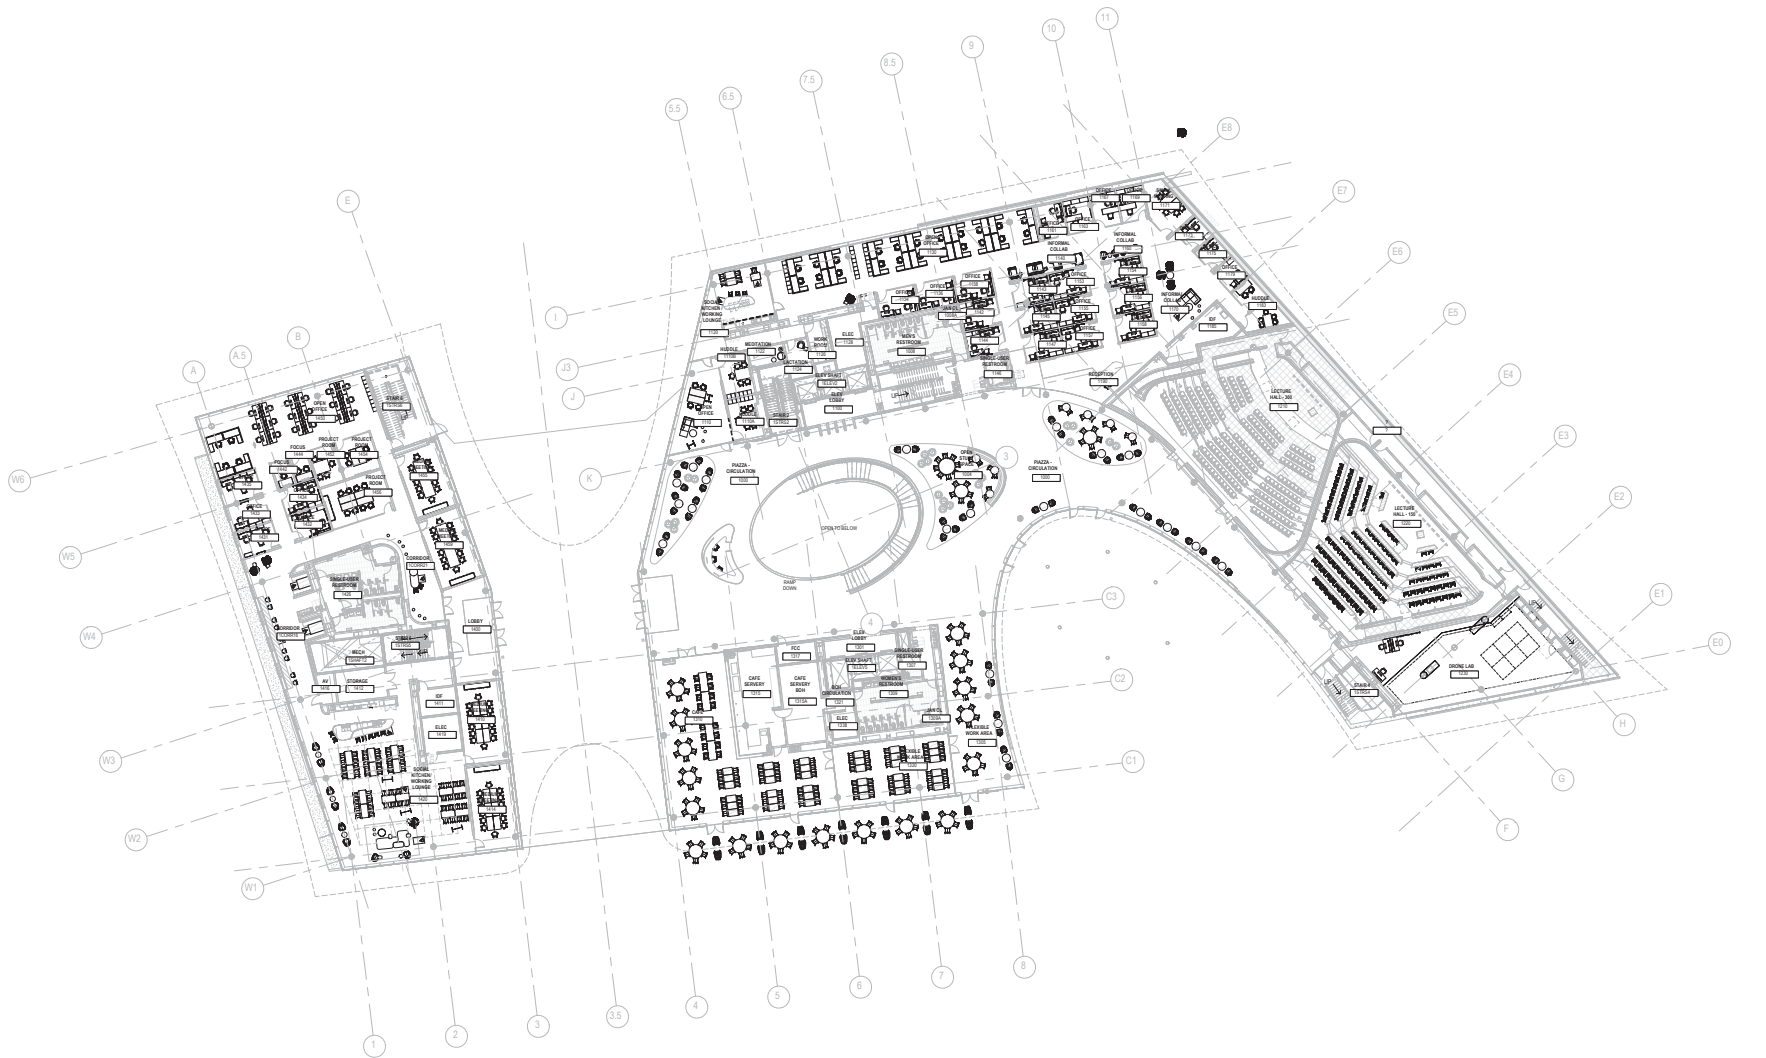

UCB Gateway Building
Berkeley CA 94720

WEISS / MANFREDI • GENSLER

ARCHITECT Manfredi 300 Lakeside Dr. 10th Floor Berkeley, CA 94702 Tel: 415.863.0000 Fax: 415.863.0001 STRUCTURAL ENGINEER SEA 1001 16th Avenue Suite 200 San Francisco, CA 94115 Tel: 415.398.0000 Fax: 415.398.0001 CIVIL ENGINEER Shaw Engineering 2000 Mission St. San Francisco, CA 94115 Tel: 415.398.0000 Fax: 415.398.0001 MECHANICAL ENGINEER Shaw Engineering 2000 Mission St. San Francisco, CA 94115 Tel: 415.398.0000 Fax: 415.398.0001 ELECTRICAL ENGINEER Shaw Engineering 2000 Mission St. San Francisco, CA 94115 Tel: 415.398.0000 Fax: 415.398.0001 PLUMBING ENGINEER Shaw Engineering 2000 Mission St. San Francisco, CA 94115 Tel: 415.398.0000 Fax: 415.398.0001	ARCHITECT Manfredi 300 Lakeside Dr. 10th Floor Berkeley, CA 94702 Tel: 415.863.0000 Fax: 415.863.0001 STRUCTURAL ENGINEER SEA 1001 16th Avenue Suite 200 San Francisco, CA 94115 Tel: 415.398.0000 Fax: 415.398.0001 CIVIL ENGINEER Shaw Engineering 2000 Mission St. San Francisco, CA 94115 Tel: 415.398.0000 Fax: 415.398.0001 MECHANICAL ENGINEER Shaw Engineering 2000 Mission St. San Francisco, CA 94115 Tel: 415.398.0000 Fax: 415.398.0001 ELECTRICAL ENGINEER Shaw Engineering 2000 Mission St. San Francisco, CA 94115 Tel: 415.398.0000 Fax: 415.398.0001 PLUMBING ENGINEER Shaw Engineering 2000 Mission St. San Francisco, CA 94115 Tel: 415.398.0000 Fax: 415.398.0001
---	---

FOR REFERENCE ONLY

Project Name
UCB Gateway

Project Number
01.4968.000

Description
FURNITURE PLAN - OVERALL - LEVEL 01

Scale
1/16" = 1'-0"

A1.601